


BIEGELISTE					
Pos.	Form und Abmessungen [cm]	Ø B550 B	lg [m]	n [Stk.]	lg [m]
029-B-Decke über EG Untere Bewehrung Teil 2					
1	270	10	2.70	16	43.20
2	130	10	1.30	18	23.40
3	125	10	1.25	11	13.75
4	735	10	7.35	7	51.45
5	270	12	2.70	4	10.80
6	600	12	6.00	9	54.00
7	60	10	1.34	163	218.42
8	60	10	1.32	154	203.28
9	140	10	1.40	9	12.60
10	1120	10	11.20	16	179.20
11	1095	10	10.95	6	65.70
12	530	10	5.30	5	26.50
13	985	10	9.85	14	137.90
14	1050	10	10.50	1	10.50
15	480	10	4.80	5	24.00
16	1000	10	10.00	22	220.00
17	1020	10	10.20	22	224.40
18	920	10	9.20	16	147.20
19	670	10	6.70	7	46.90
20	645	10	6.45	3	19.35
21	495	10	4.95	1	4.95
22	590	10	5.90	25	147.50
23	425	10	4.25	10	42.50
24	335	10	3.35	4	13.40
25	700	10	7.00	15	105.00
26	720	10	7.20	11	79.20
27	600	10	6.00	2	12.00
28	585	10	5.85	28	163.80
29	390	10	3.90	23	89.70
30	360	10	3.60	5	18.00
31	970	10	9.70	8	77.60
32	155	10	1.55	229	354.95
33	855	10	8.55	8	68.40
34	795	10	7.95	8	63.60
35	820	10	8.20	8	65.60
36	955	10	9.55	8	76.48
37	908	10	9.08	10	90.80
38	200	10	2.00	2	4.00
39	150	10	1.50	10	15.00
40	60	10	1.29	81	104.49
41	100	10	1.00	2	2.00
42	565	10	5.65	2	11.30
43	180	10	1.80	2	3.60
44	60	10	1.31	102	133.62
45	60	10	1.36	8	10.88
46	360	12	3.60	2	7.20
47	381	12	5.28	2	10.56

BIEGELISTE					
Pos.	Form und Abmessungen [cm]	Ø B550 B	lg [m]	n [Stk.]	lg [m]
029-B-Decke über EG Untere Bewehrung Teil 2					
48	629	12	7.76	2	15.52
49	470	14	4.70	2	9.40
50	855	14	8.55	2	17.10
51	407	14	5.54	2	11.08
52	350	14	4.97	2	9.94
53	828	16	9.75	2	19.50
54	795	14	7.95	2	15.90
55	666	16	8.11	4	32.44
56	306	12	4.53	2	9.06
57	720	14	7.20	2	14.40
58	970	14	9.70	2	19.40
59	93	12	2.40	7	16.80
60	377	14	5.24	2	10.48
61	955	14	9.55	2	19.10
62	287	12	4.14	2	8.28
63	450	12	4.50	5	22.50
64	370	12	3.70	7	25.90
65	250	12	2.50	6	15.00
66	15	8	0.40	147	58.80
67	95	10	2.30	355	816.50
68	80	8	1.94	330	640.20
69	110	14	2.75	15	41.25
70	110	16	9.42	2	18.84
71	817	12	1.50	26	39.00
72	70	8	0.91	36	32.76
73	40	8	0.90	24	21.60
74	170	10	1.70	4	6.80
75	40	8	0.94	20	18.80
76	40	8	0.92	48	44.16
77	680	12	6.80	2	13.60
78	400	12	4.00	2	8.00
79	110	12	2.66	2	5.32
80	95	10	1.24	3	3.72


STECKER DET.A

l=52,6m M 1:25

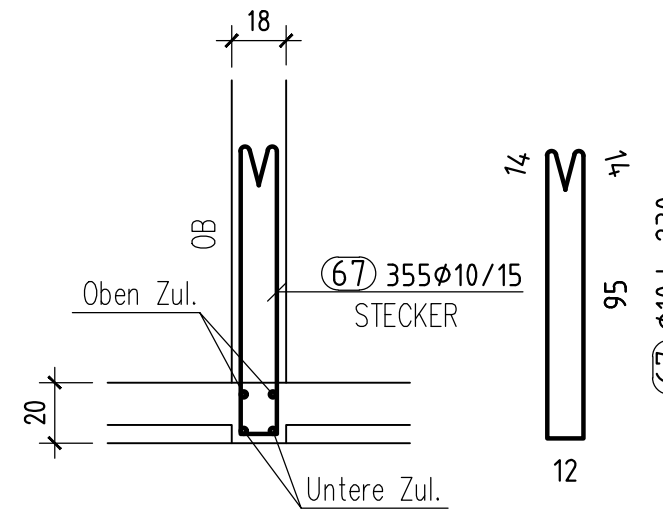


STECKER DET.B

l=49,5m M 1:25

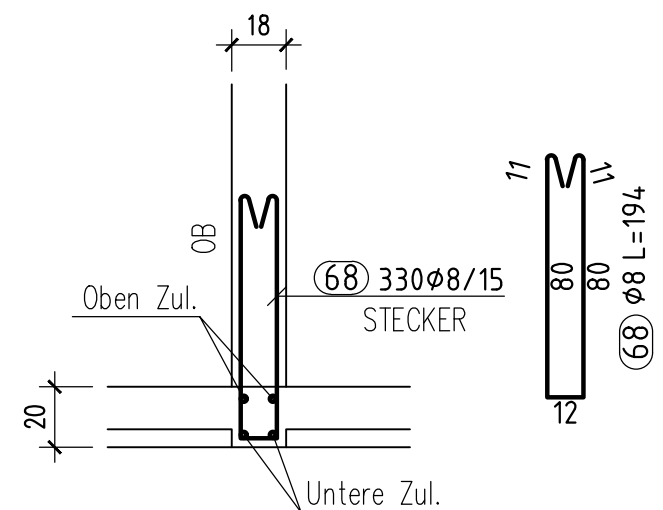

DET.C


M 1:25

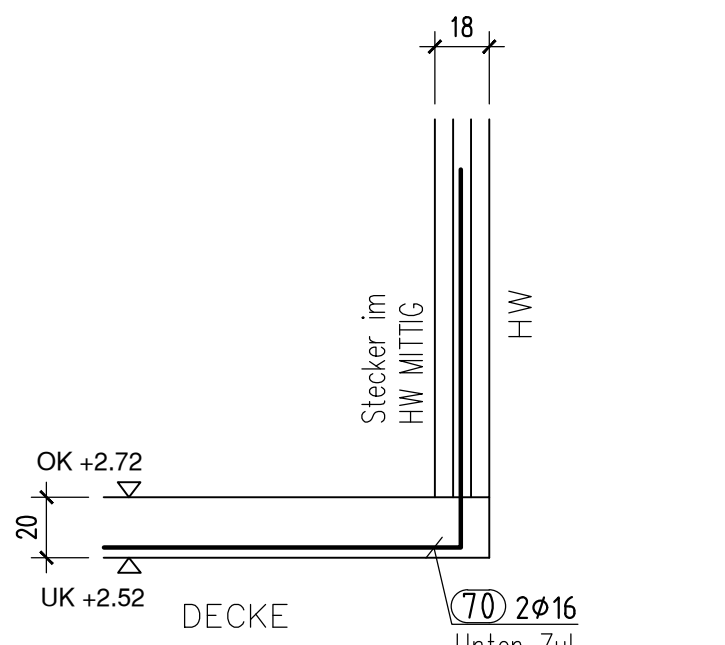

ZUSAMMENSTELLUNG DER BIEGELISTE

Ø [mm]	lg [m]	Gewicht pro m' [kg/m']	Gewicht [kg]
BSI 550			
8	816.32	0.40	322.45
10	4253.14	0.62	2624.19
12	261.54	0.89	232.25
14	168.05	1.21	203.34
16	70.78	1.58	111.83
Gesamtgewicht [kg] (BSI 550)			3494.05
Gesamtgewicht [kg]			3494.05

UNTERE BEWEHRUNG

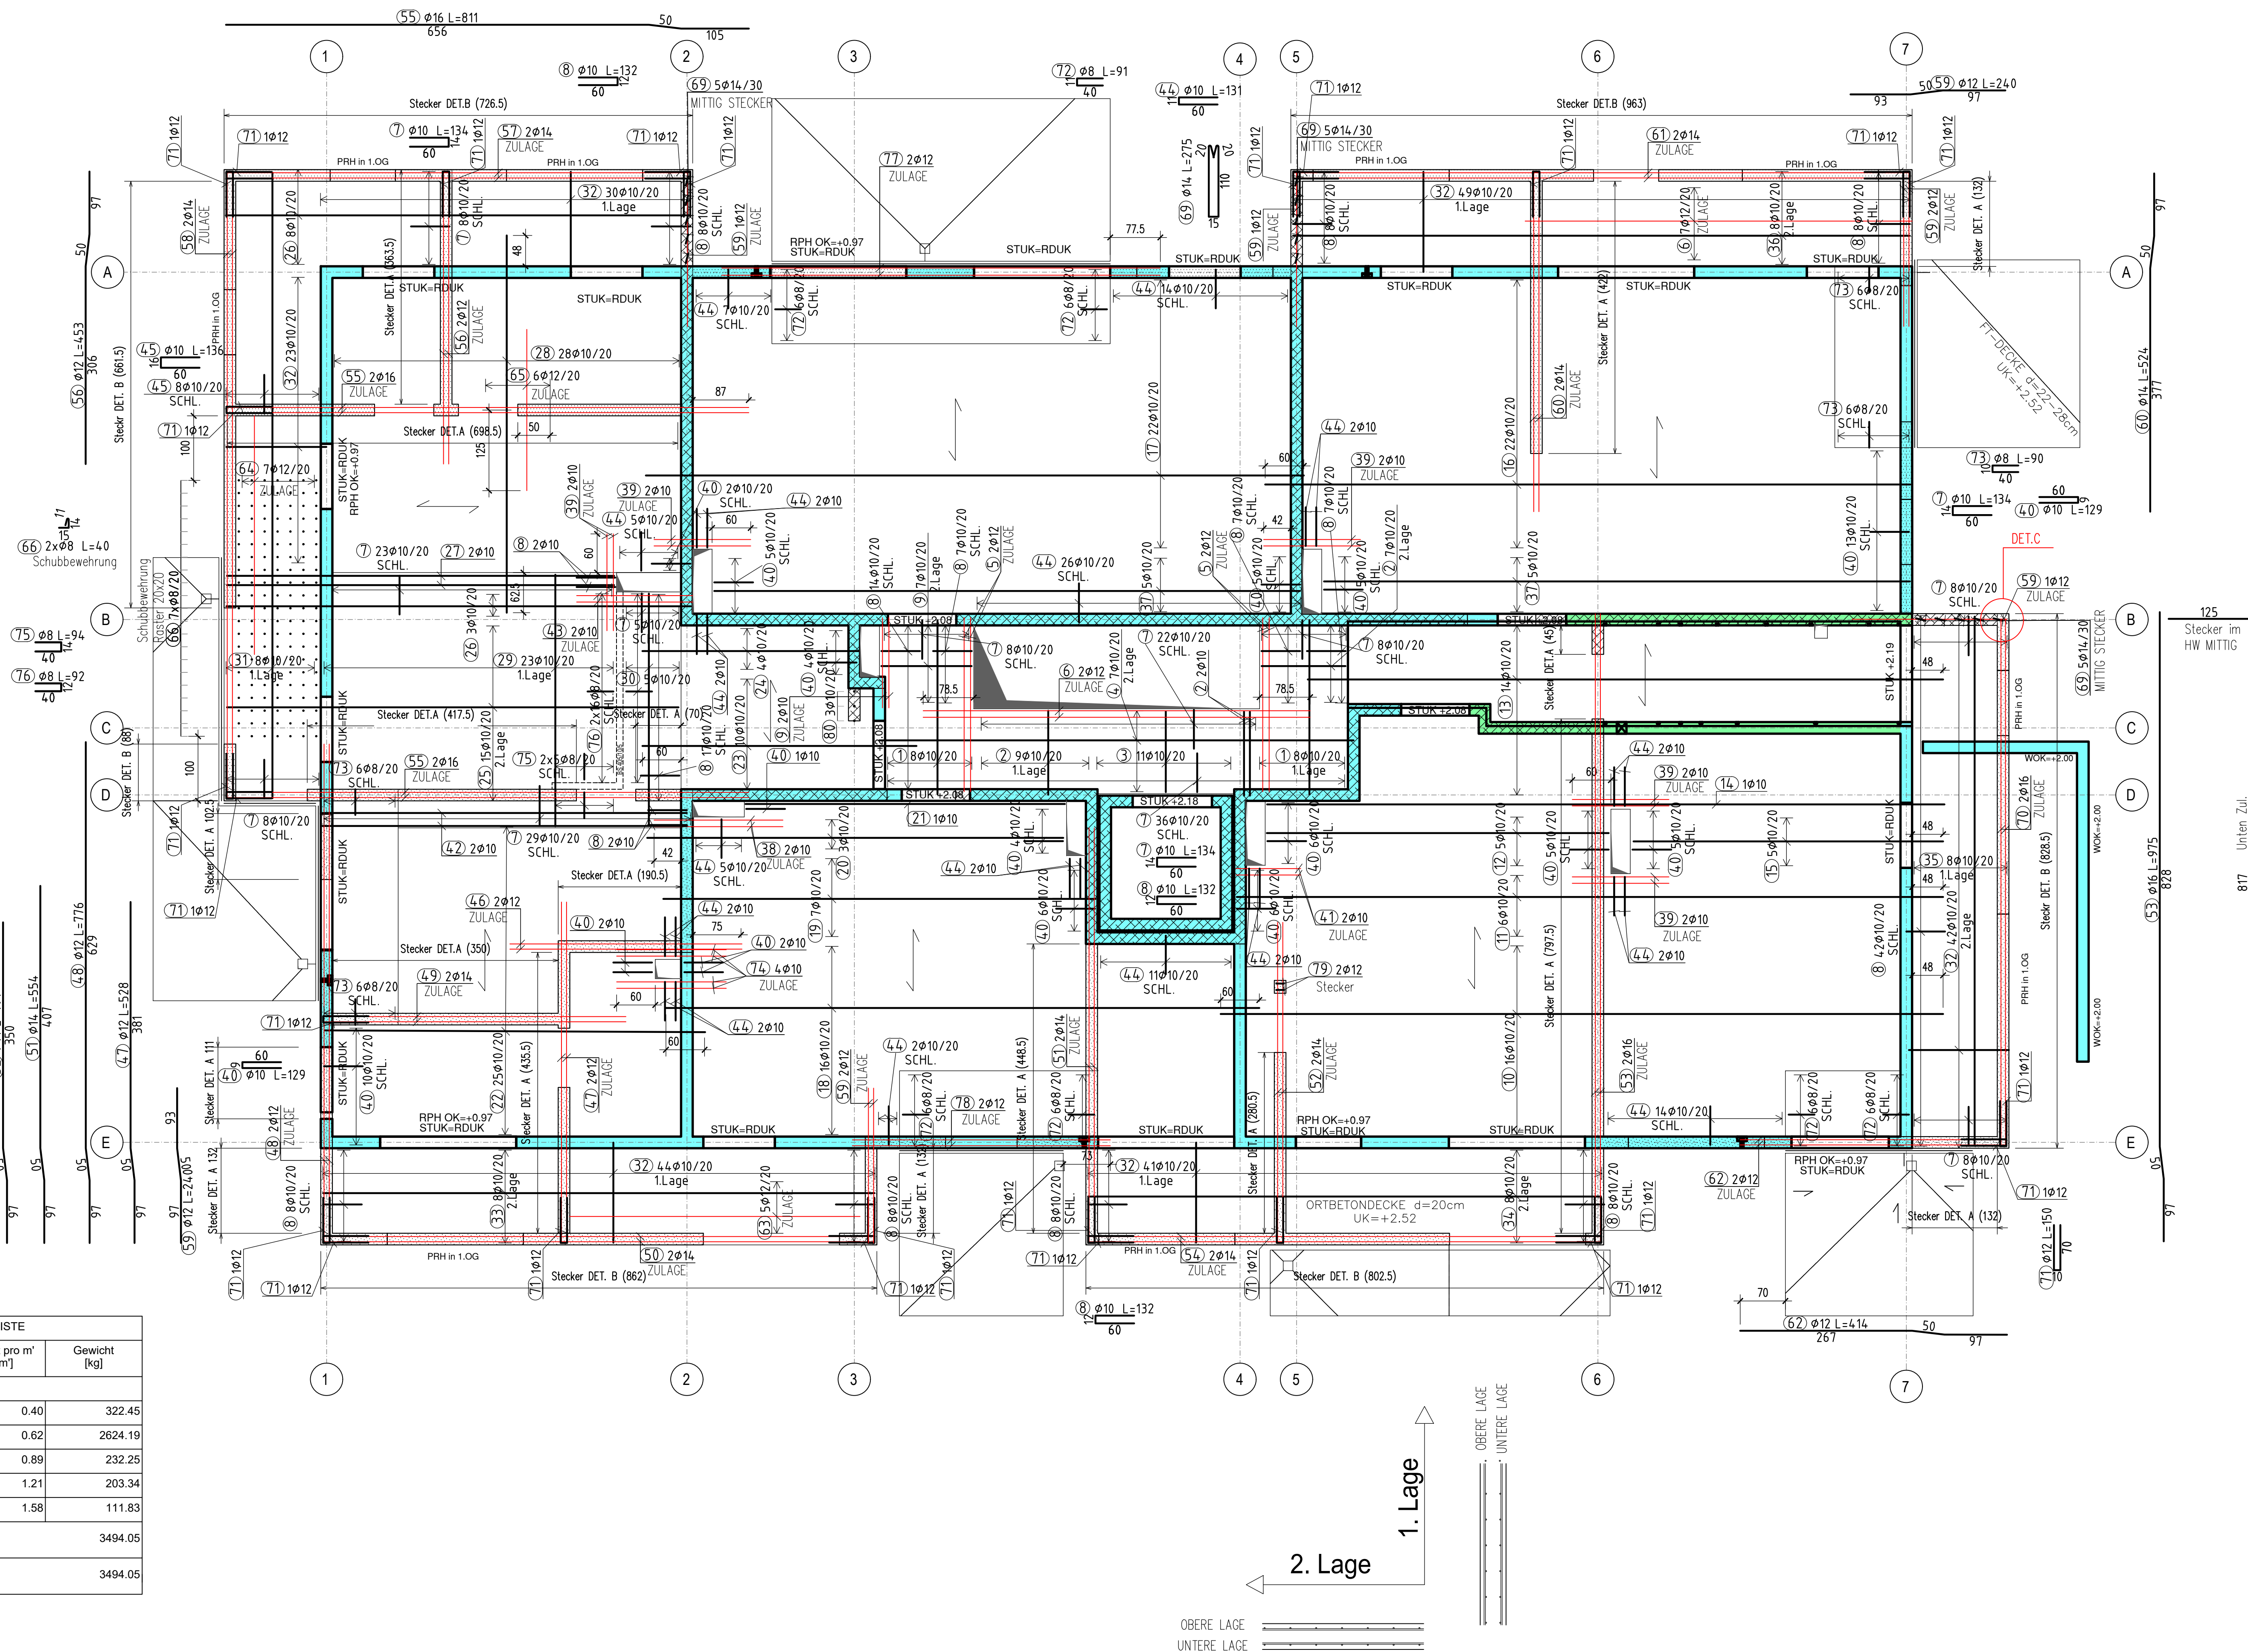


BETON

Betonfestigkeitsklasse: C25/30
Expositionsklasse: XC1

Vom Planverfasser werden die Betonfestigkeitsklasse sowie die Expositionsklasse gemäß ÖNORM B4710-1 vorgegeben. Es gelten die landesspezifischen Regelungen für Österreich (A). Die sonstigen Betoneigenschaften sind vom Besteller entsprechend den jeweiligen Anforderungen festzulegen. Für Verarbeitung und Nachbehandlung sind die Anforderungen der ÖNORM B4710-1 einzuhalten.

BETONDECKUNG: c=3,0cm

DETAIL AUFBIEGUNGEN

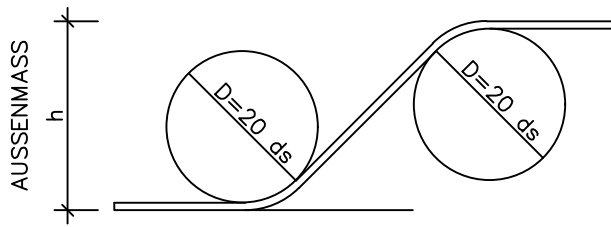

BEWEHRUNGSSTAHL

Mindestbiegerolldurchmesser
Stabstahl: BSI550A Stabdurchmesser Ø m, min
Mattenstahl: BSI550M Ø 16mm
Die Bewehrung der Biegeformen erfolgt gemäß ÖNORM A6220 bzw. ÖNORM ISO 3766. Die angegebenen Maße sind wenn nicht anders angegeben Außenabmessungen.

UNFALLSCHUTZ

Geräte nach oben endende Stäbe (Steckelsen) müssen abgedeckt oder zusätzlich hakenförmig abgebogen werden. Dies hat ohne Verringerung der Hoftümpfe zu erfolgen.

NATURMASSE NEHMEN

INDEX	DATUM	GEZ.	GEPR.	ÄNDERUNGEN
A04				
A03				
A02				
A01				

PROJEKT: NEUBAU EINER WOHNHAUSANLAGE
UND REIHENHAUSER MIT TIEFGARAGE
1220 Wien, Am Freihof 7-9

GRST.NR.: 39/1
EZ.: 1184
KAT.GEM.: Kagr (01660)

PLANVERFASSER:



BAUHERR:

3SI Am Freihof GmbH & Co KG
Getegthofstrasse 7, 1010 Wien

PLANINHALT:
**Decke über EG
Untere Bewehrung Teil 2**

ZUGEHÖRIGE PLÄNE:

GEZEICHNET: SP	SACHBEARBEITER: KM	STATIK: KM
DATUM: 18.01.2024	MASSSTAB: 1:50	FORMAT: 60/135
GZ.NR.: 22-357	PLANNUMMER: 029	INDEX: A00

DATEINAME: 029-B-Decke über EG Untere Bewehrung Teil 2