BIEGELISTE

Pos.	Form und Abmessungen [cm]	Ø B550 B	lg [m]	n [Stk.]	lg [m]
034-B-Wände im 1.OG Bewehrung Teil 2					
1	40 / 10 / 40	8	0.90	746	671.40
2	284 / 11	8	2.95	546	1610.70
3	50 / 12 / 50	8	1.12	303	339.36
4	120 / 11	8	1.31	162	212.22
5	15 / 10 / 10 / 5 / 9.	8	0.35	1110	388.50
6	282 / 11	8	2.93	178	521.54
7	107 / 12 / 107	8	2.26	45	101.70
8	109 / 12 / 109	8	2.30	79	181.70
9	40 / 10 / 10 / 11 / 40	8	1.22	234	285.48
10	715	8	7.15	16	114.40
11	155	8	1.55	20	31.00
12	165	8	1.65	20	33.00
13	66. / 10 / 10 / 11 / 66.	8	1.74	11	19.14
14	220	12	2.20	18	39.60
15	340	12	3.40	6	20.40
16	284 / 17	12	3.01	144	433.44
17	282 / 17	12	2.99	26	77.74
18	440	8	4.40	8	35.20
19	140	8	1.40	28	39.20
20	280	8	2.80	28	78.40
21	99. / 12 / 11 / 12 / 99.	8	2.44	8	19.52
22	35 / 12 / 11 / 12 / 35	8	1.16	18	20.88
23	875	12	8.75	2	17.50
24	286 / 11	8	2.97	18	53.46
25	285	12	2.85	19	54.15
26	10 / 105 / 11	8	1.26	180	226.80
27	286 / 17	12	3.03	2	6.06
28	455	8	4.55	16	72.80
29	215	8	2.15	18	38.70
30	385	8	3.85	36	138.60
31	23 / 12 / 11 / 12 / 23	8	0.92	11	10.12
32	300	12	3.00	12	36.00
33	550	12	5.50	2	11.00
34	46 / 12 / 11 / 12 / 46	8	1.38	10	13.80
35	70 / 12 / 70	12	1.52	28	42.56
36	320	12	3.20	2	6.40
37	20 / 12 / 14 / 12 / 20	10	0.92	15	13.80
38	380	14	3.80	2	7.60
39	350	12	3.50	8	28.00
40	170 / 17	12	1.87	20	37.40
41	400	10	4.00	36	144.00
42	83 / 12 / 14 / 12 / 83	10	2.18	18	39.24
43	12 / 12 / 11 / 12 / 12	8	0.70	18	12.60
44	185	12	1.85	2	3.70
45	875	8	8.75	4	35.00
46	185	10	1.85	4	7.40
47	220	10	2.20	44	96.80
48	200	10	2.00	36	72.00
49	58 / 12 / 14 / 12 / 58	10	1.68	18	30.24
50	70 / 10 / 70	12	1.50	23	34.50
51	40 / 10 / 14 / 10 / 40	10	1.28	7	8.96
52	284 / 14	10	2.98	324	965.52
53	140 / 14	10	1.54	28	43.12
54	60 / 12 / 60	10	1.32	192	253.44
55	50 / 10 / 50	10	1.10	224	246.40
56	340	8	3.40	4	13.60
57	230	8	2.30	12	27.60
58	300	8	3.00	44	132.00
59	550	8	5.50	4	22.00
60	282 / 14	10	2.96	72	213.12
61	380	10	3.80	36	136.80
62	245	8	2.45	40	98.00
63	89 / 10 / 11 / 10 / 89	8	2.20	8	17.60
64	115 / 10 / 12 / 8	8	1.45	8	11.60
65	118 / 10 / 11 / 10 / 118	8	2.78	29	80.62
66	36 / 10 / 11 / 10 / 36	8	1.14	7	7.98
67	50 / 12 / 11 / 12 / 50	8	1.46	8	11.68
68	180	10	1.80	22	39.60
69	95 / 10 / 14 / 10 / 95	10	2.38	8	19.04
70	63 / 10 / 14 / 10 / 63	10	1.74	8	13.92
71	120	10	1.20	44	52.80
72	520	12	5.20	2	10.40
73	520	8	5.20	4	20.80
74	52 / 12 / 14 / 12 / 52	10	1.56	18	28.08
75	585	8	5.85	16	93.60
76	86 / 12 / 11 / 12 / 86	8	2.18	10	21.80
77	330	12	3.30	8	26.40
78	330	8	3.30	12	39.60
79	525	8	5.25	7	36.75
80	555 / 12 / 10 / 8	8	5.85	7	40.95
81	81 / 12 / 11 / 12 / 81	8	2.08	28	58.24
82	615	8	6.15	8	49.20
83	180	8	1.80	20	36.00
84	220	8	2.20	12	26.40
85	670	8	6.70	8	53.60
86	325	8	3.25	22	71.50
87	22 / 12 / 14 / 12 / 22	10	0.96	19	18.24
88	14 / 12 / 11 / 12 / 14	8	0.74	18	13.32
89	375	8	3.75	36	135.00
90	430	8	4.30	38	163.40
91	145	8	1.45	8	11.60
92	170 / 10 / 12 / 8	8	2.00	8	16.00
93	170	8	1.70	22	37.40
94	114 / 12 / 11 / 12 / 114	8	2.74	10	27.40
95	450	8	4.50	36	162.00
96	130	8	1.30	36	46.80
97	225	8	2.25	36	81.00
98	130	10	1.30	36	46.80
99	160	8	1.60	36	57.60
100	460	8	4.60	36	165.60
101	285	8	2.85	36	102.60
102	175	14	1.75	2	3.50
103	175	10	1.75	8	14.00
104	12 / 12 / 14 / 12 / 12	10	0.76	16	12.16
105	785	10	7.85	36	282.60
106	109 / 12 / 109	10	2.30	19	43.70
107	270	8	2.70	20	54.00
108	815	8	8.15	16	130.40
109	815 / 60	14	8.75	2	17.50
110	60 / 105	14	1.65	2	3.30
111	123 / 12 / 11 / 12 / 123	8	2.92	10	29.20
112	80 / 15 / 80	10	1.75	9	15.75
113	75 / 12 / 11 / 12 / 75	8	1.96	10	19.60
114	128	8	1.28	20	25.60
115	36 / 12 / 11 / 12 / 36	8	1.18	8	9.44
116	360	8	3.60	4	14.40
117	360	12	3.60	2	7.20
118	580	12	5.80	2	11.60
119	580	8	5.80	4	23.20
120	340 / 11	8	3.51	30	105.30
121	245	12	2.45	2	4.90
122	260	10	2.60	36	93.60
123	58 / 12 / 17 / 12 / 58	12	1.74	12	20.88

ZUSAMMENSTELLUNG DER BIEGELISTE

Ø [mm]	lg [m]	Gewicht pro m' [kg/m']	Gewicht [kg]
BSt 550			
8	7707.20	0.40	3044.34
10	2951.13	0.62	1820.85
12	929.83	0.89	825.69
14	31.90	1.21	38.60
Gesamtgewicht [kg] (BSt 550)			5729.48
Gesamtgewicht [kg]			5729.48

Wand 1

d=18cm M 1:50
C 25/30 XC1

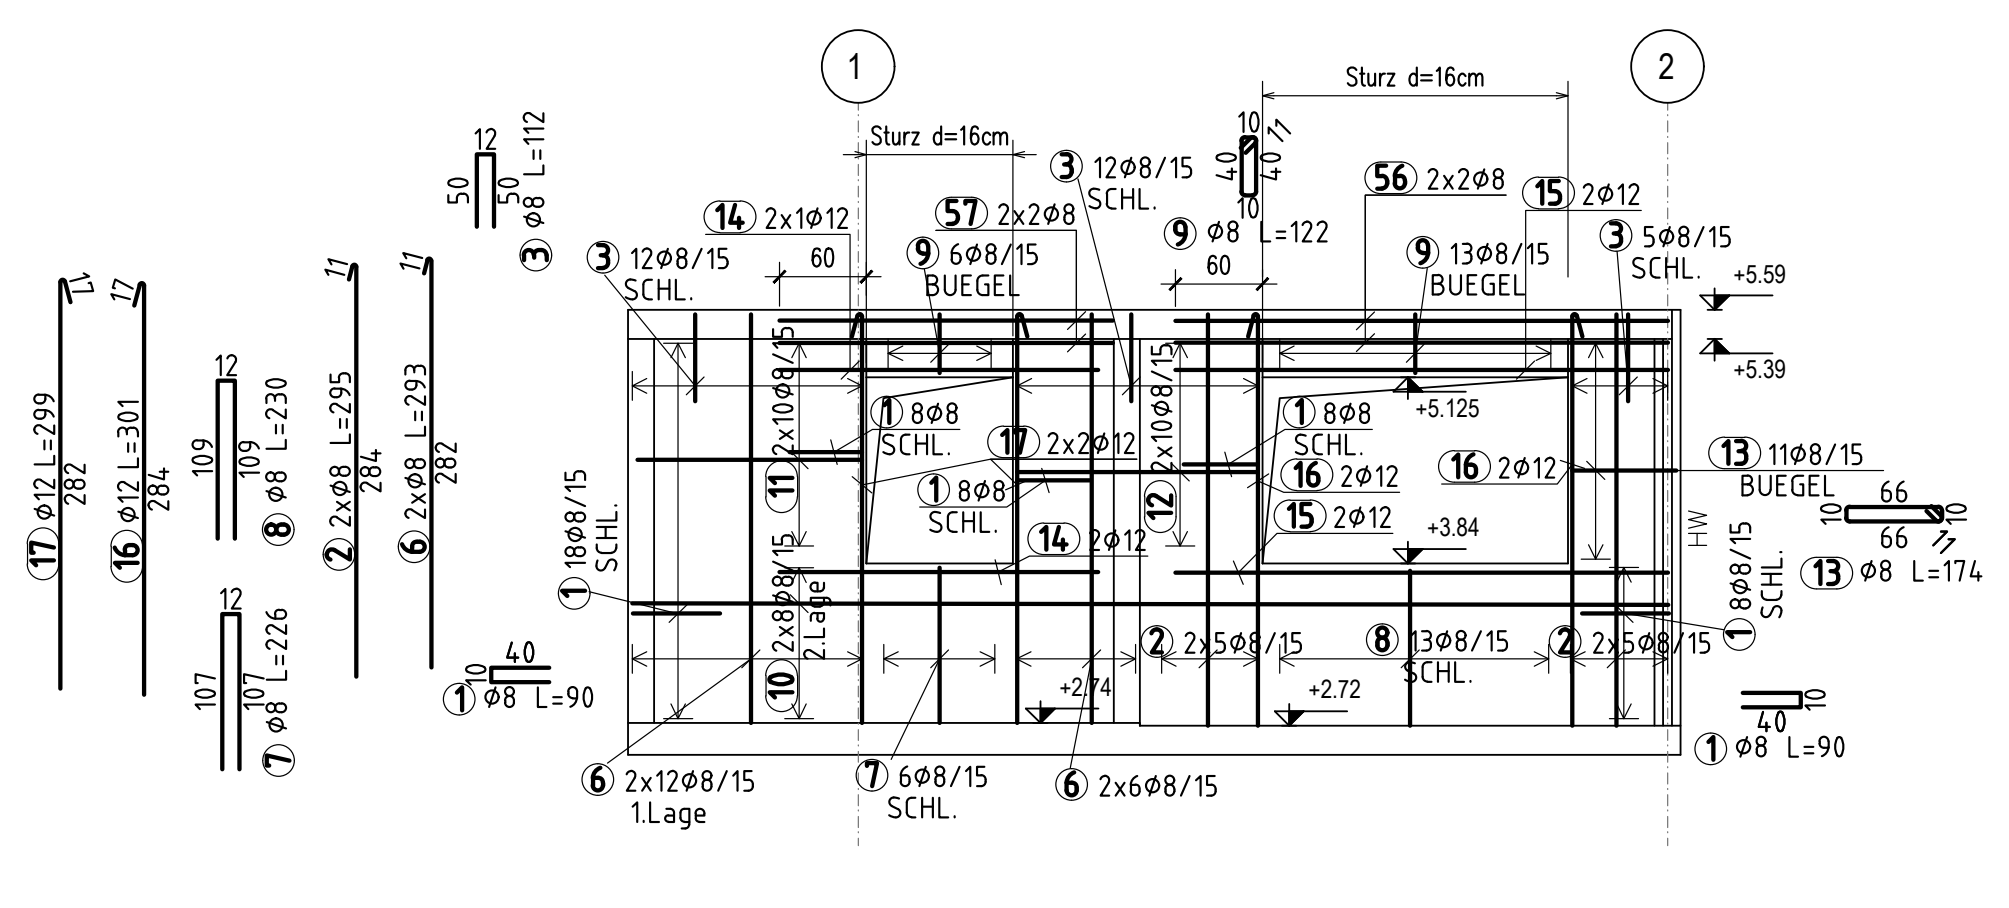

Wand 2

d=18cm M 1:50
C 25/30 XC1

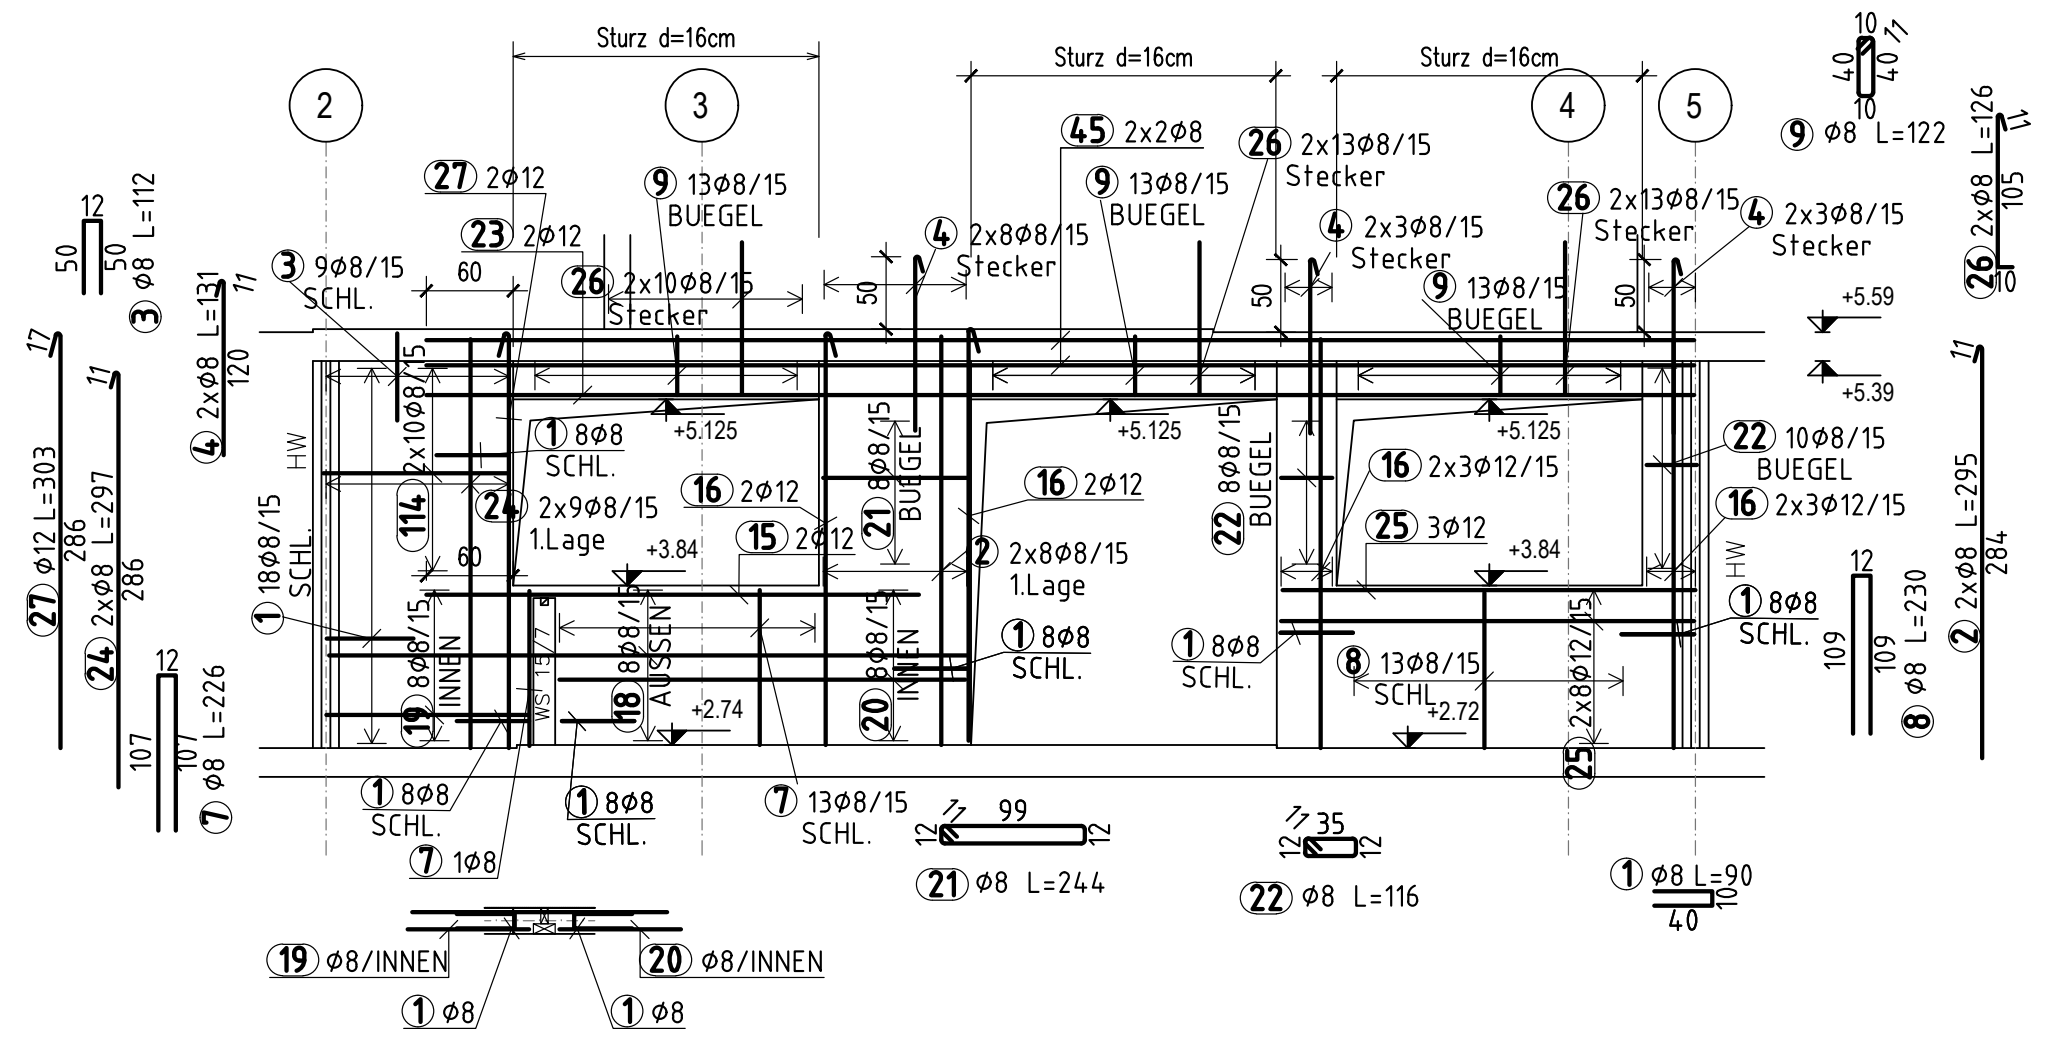

Wand 3

d=18cm M 1:50
C 25/30 XC1

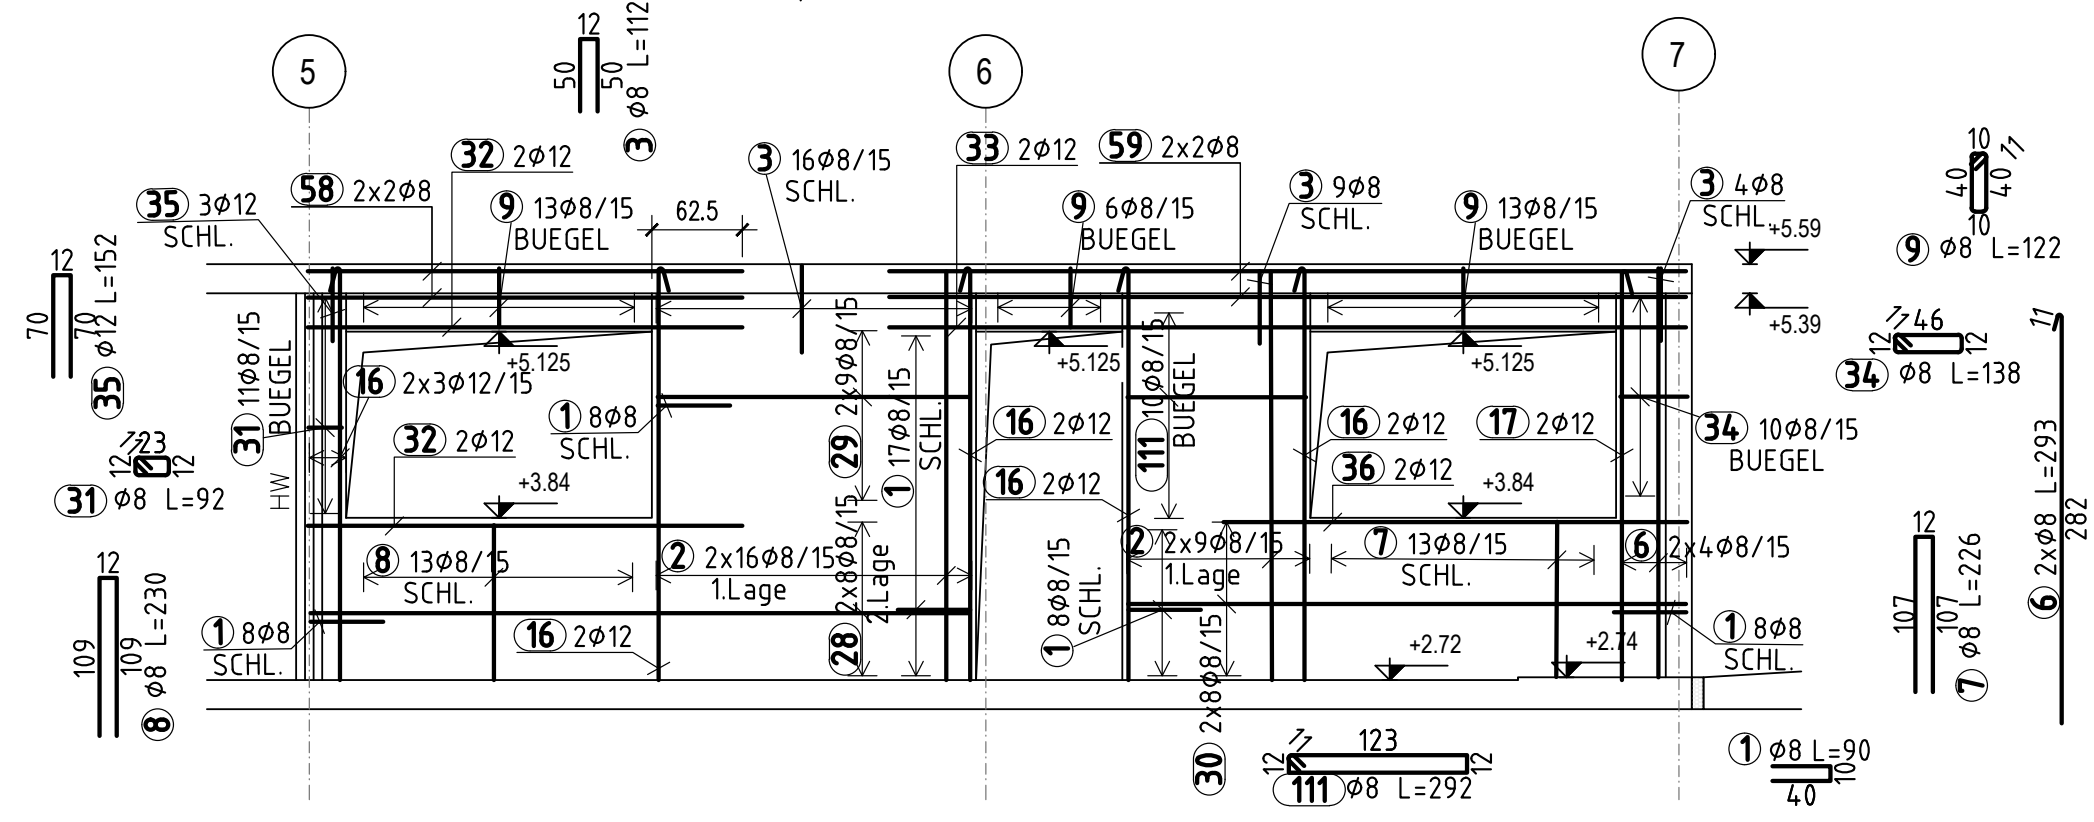

Wand 4

d=18cm M 1:50
C 25/30 XC1

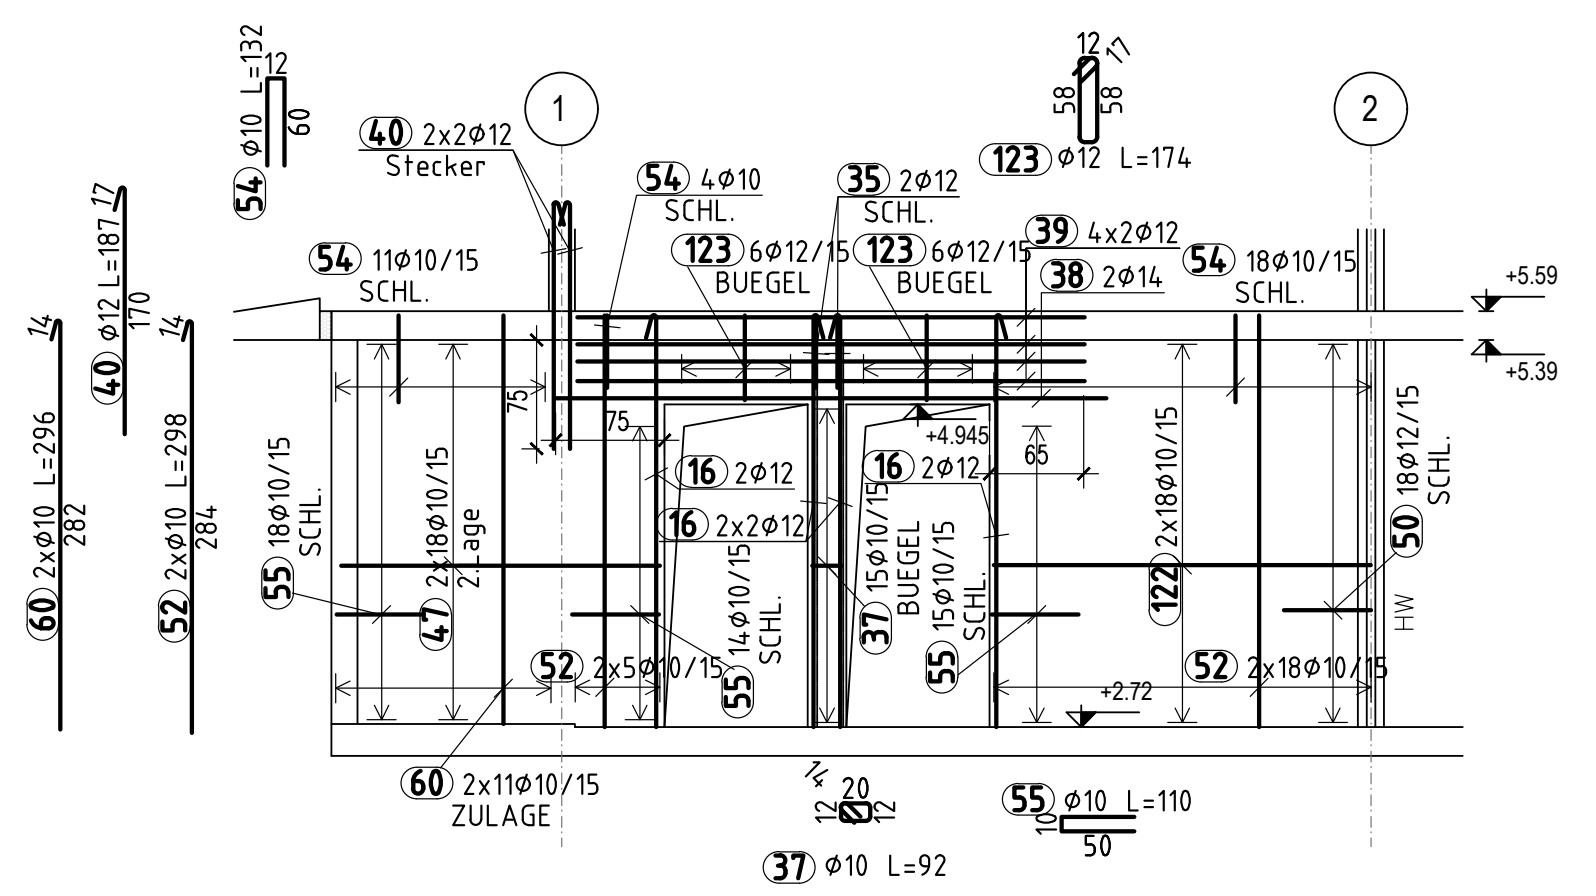

Wand 5

d=18cm M 1:50
C 25/30 XC1

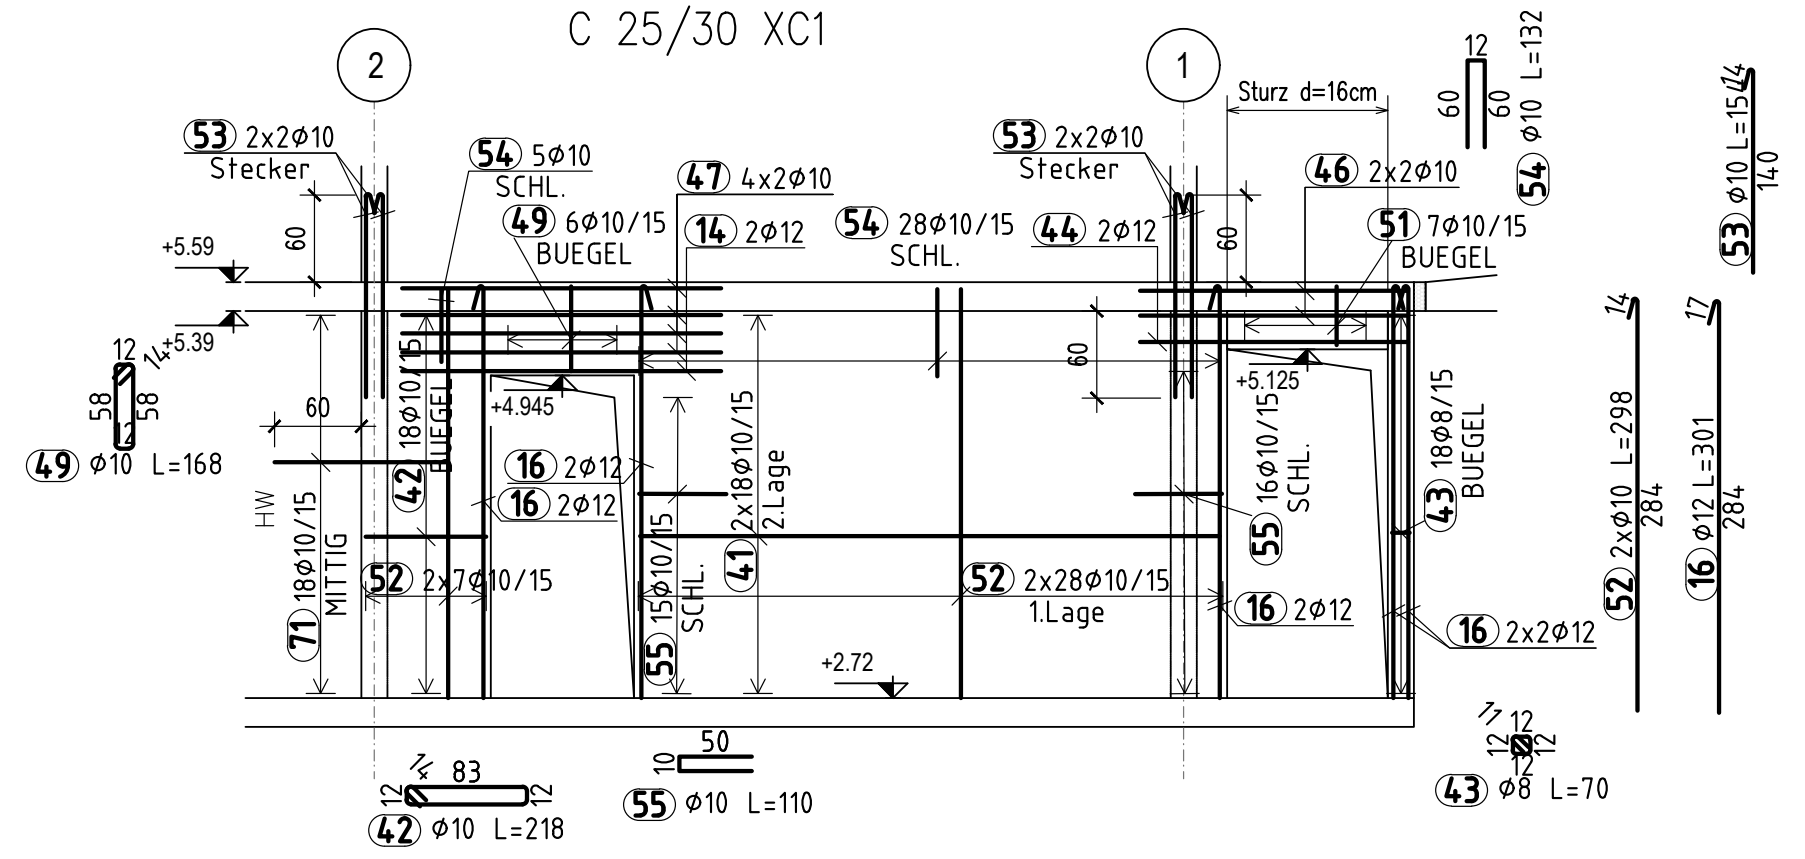

Wand 6

d=18cm M 1:50
C 25/30 XC1

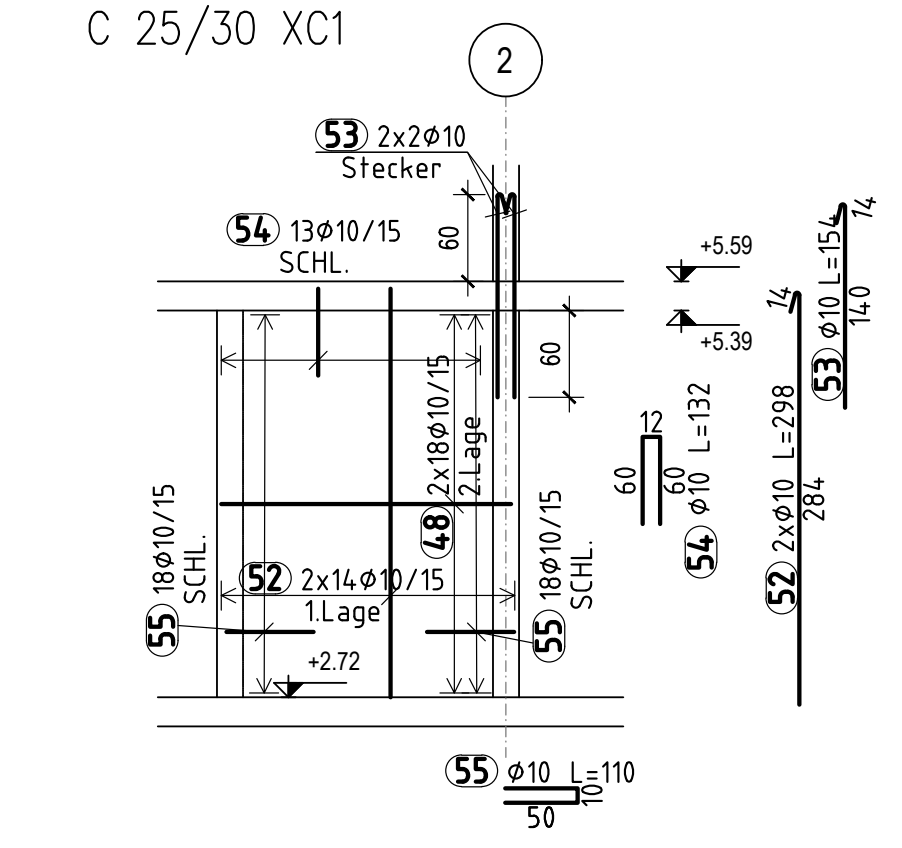

Wand 7

d=18cm M 1:50
C 25/30 XC1

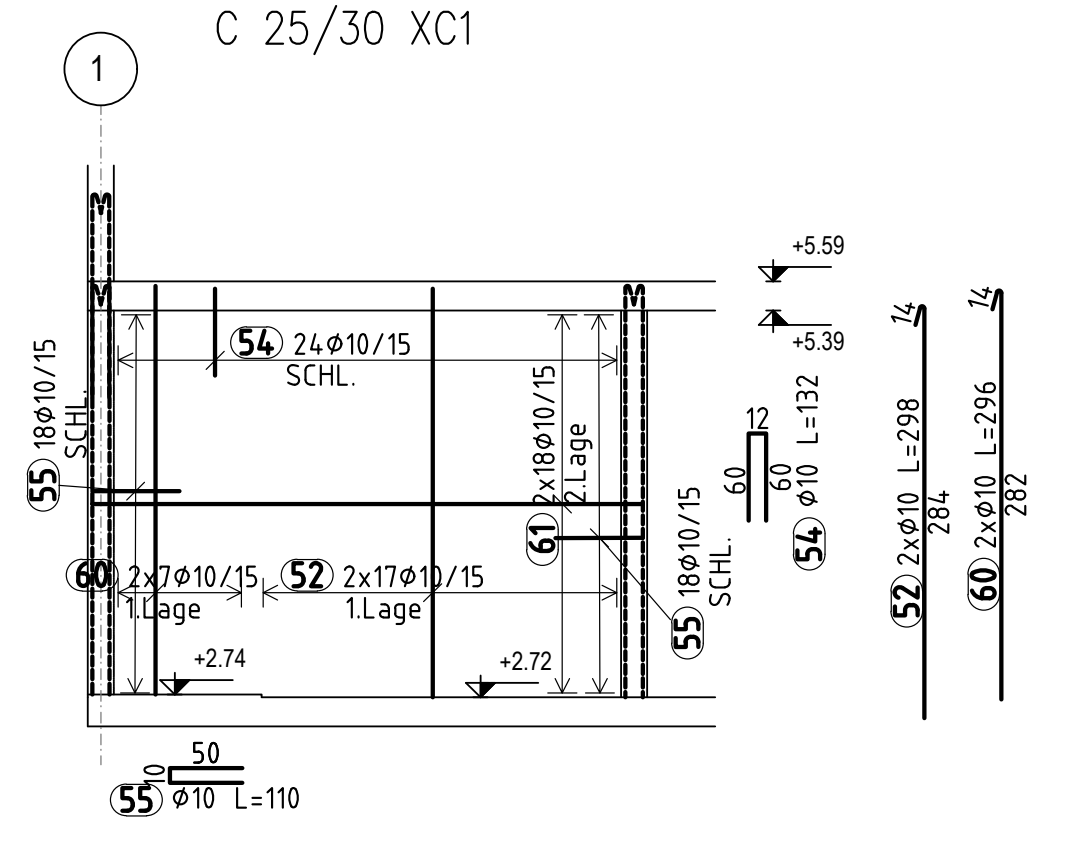

Wand 8

d=18cm M 1:50
C 25/30 XC1

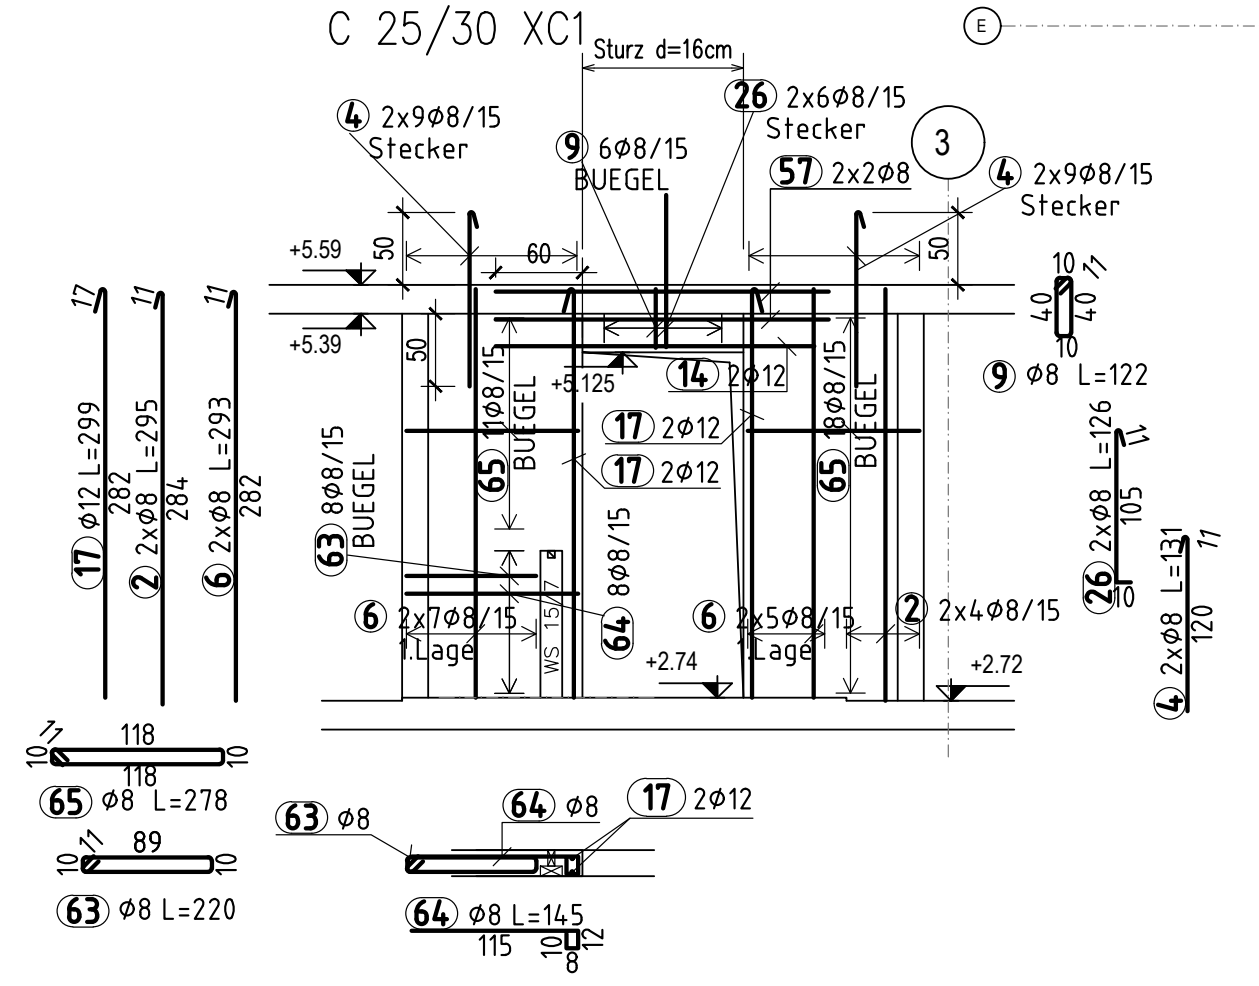

Wand 9

d=18cm M 1:50
C 25/30 XC1

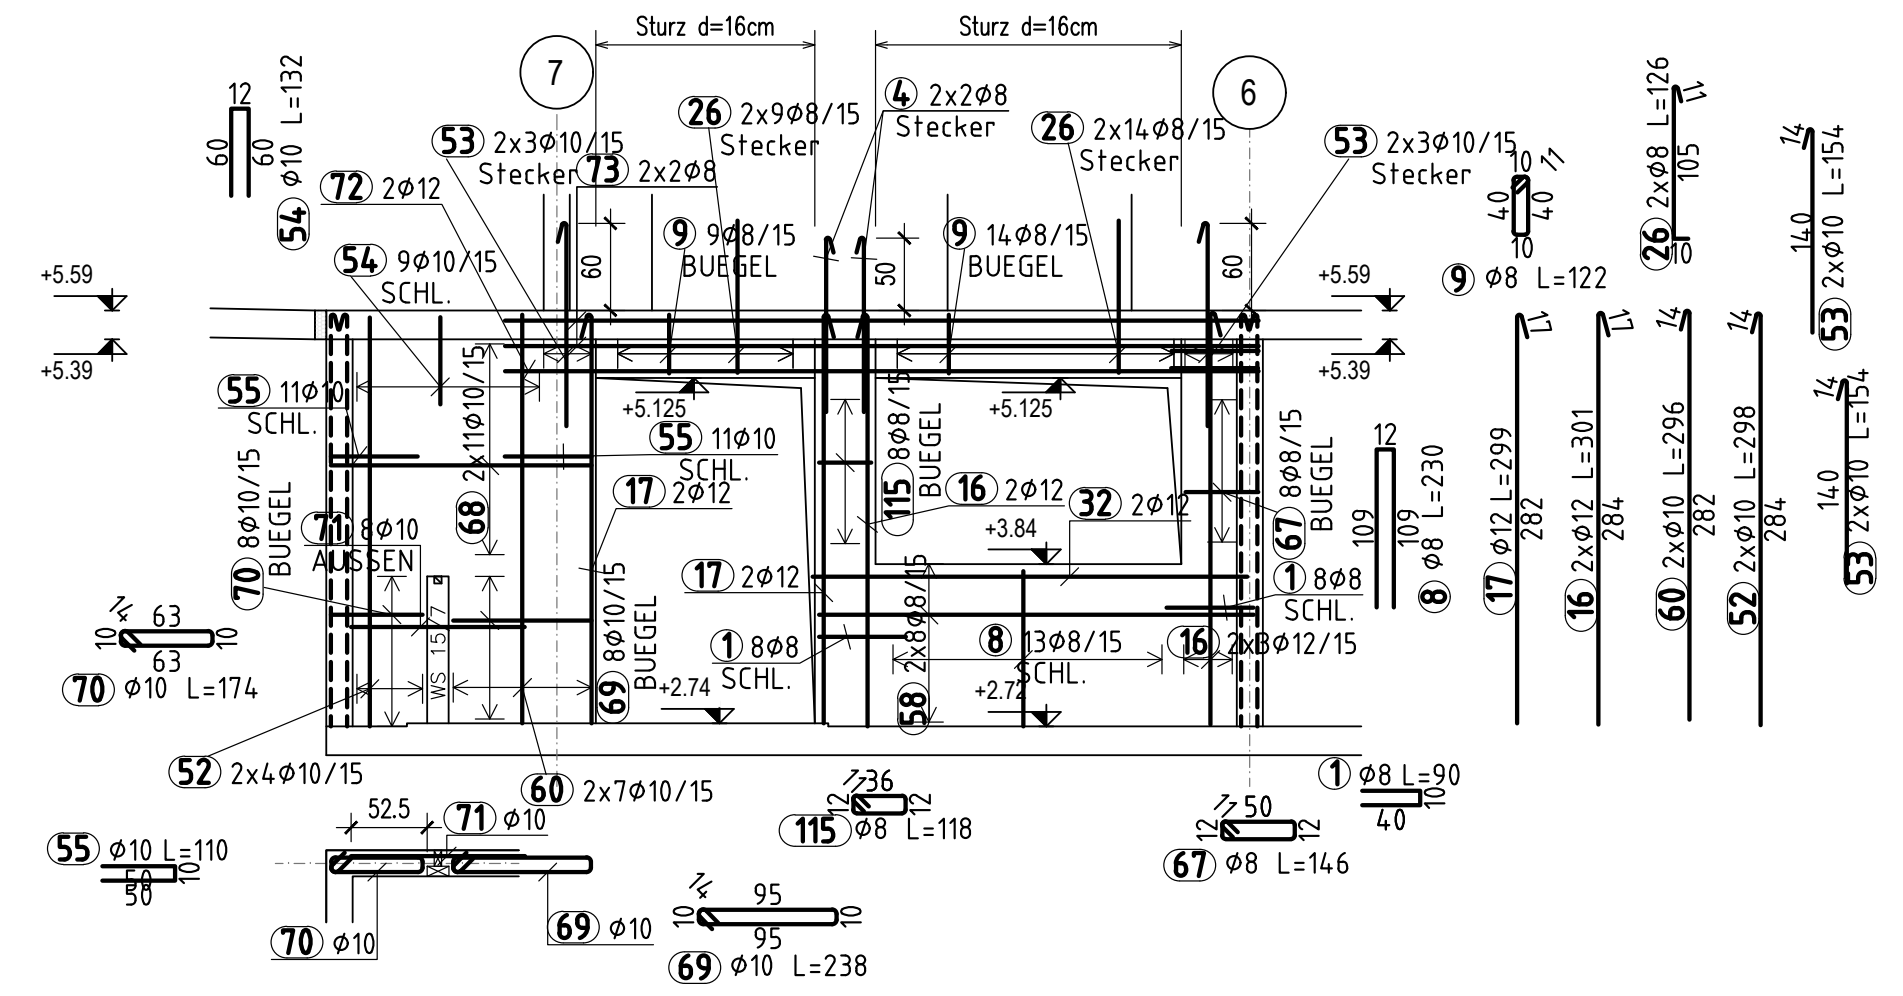

Wand 10

d=18cm M 1:50
C 25/30 XC1

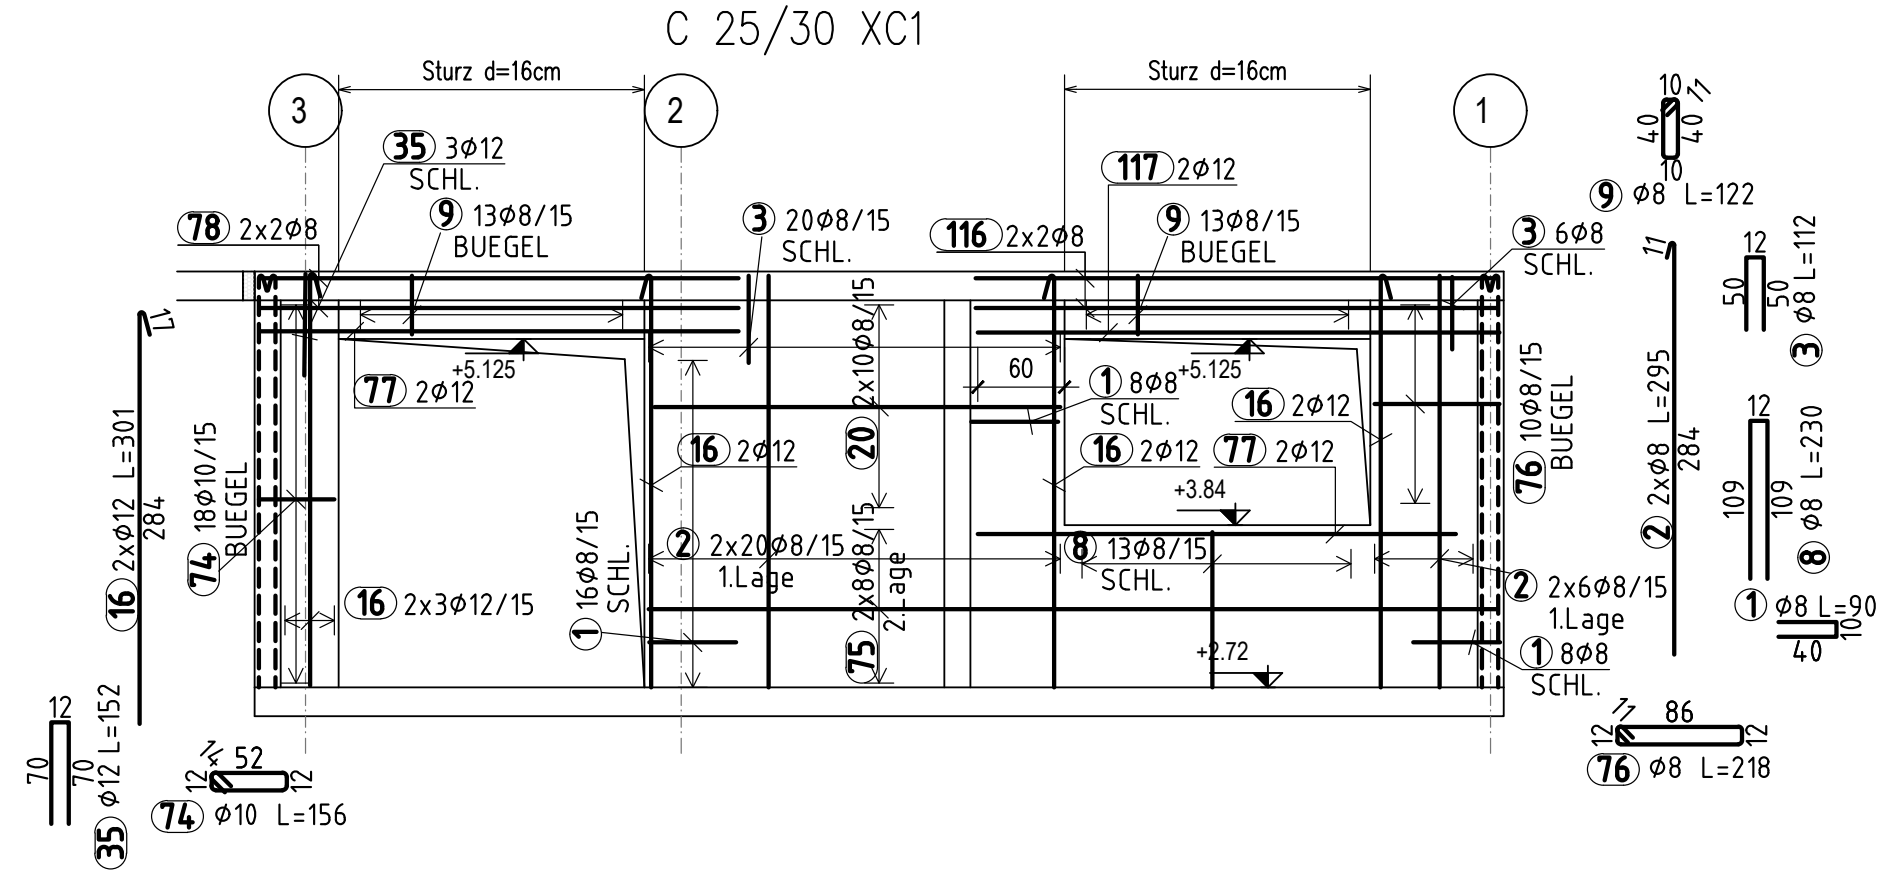

Wand 11

d=18cm M 1:50
C 25/30 XC1

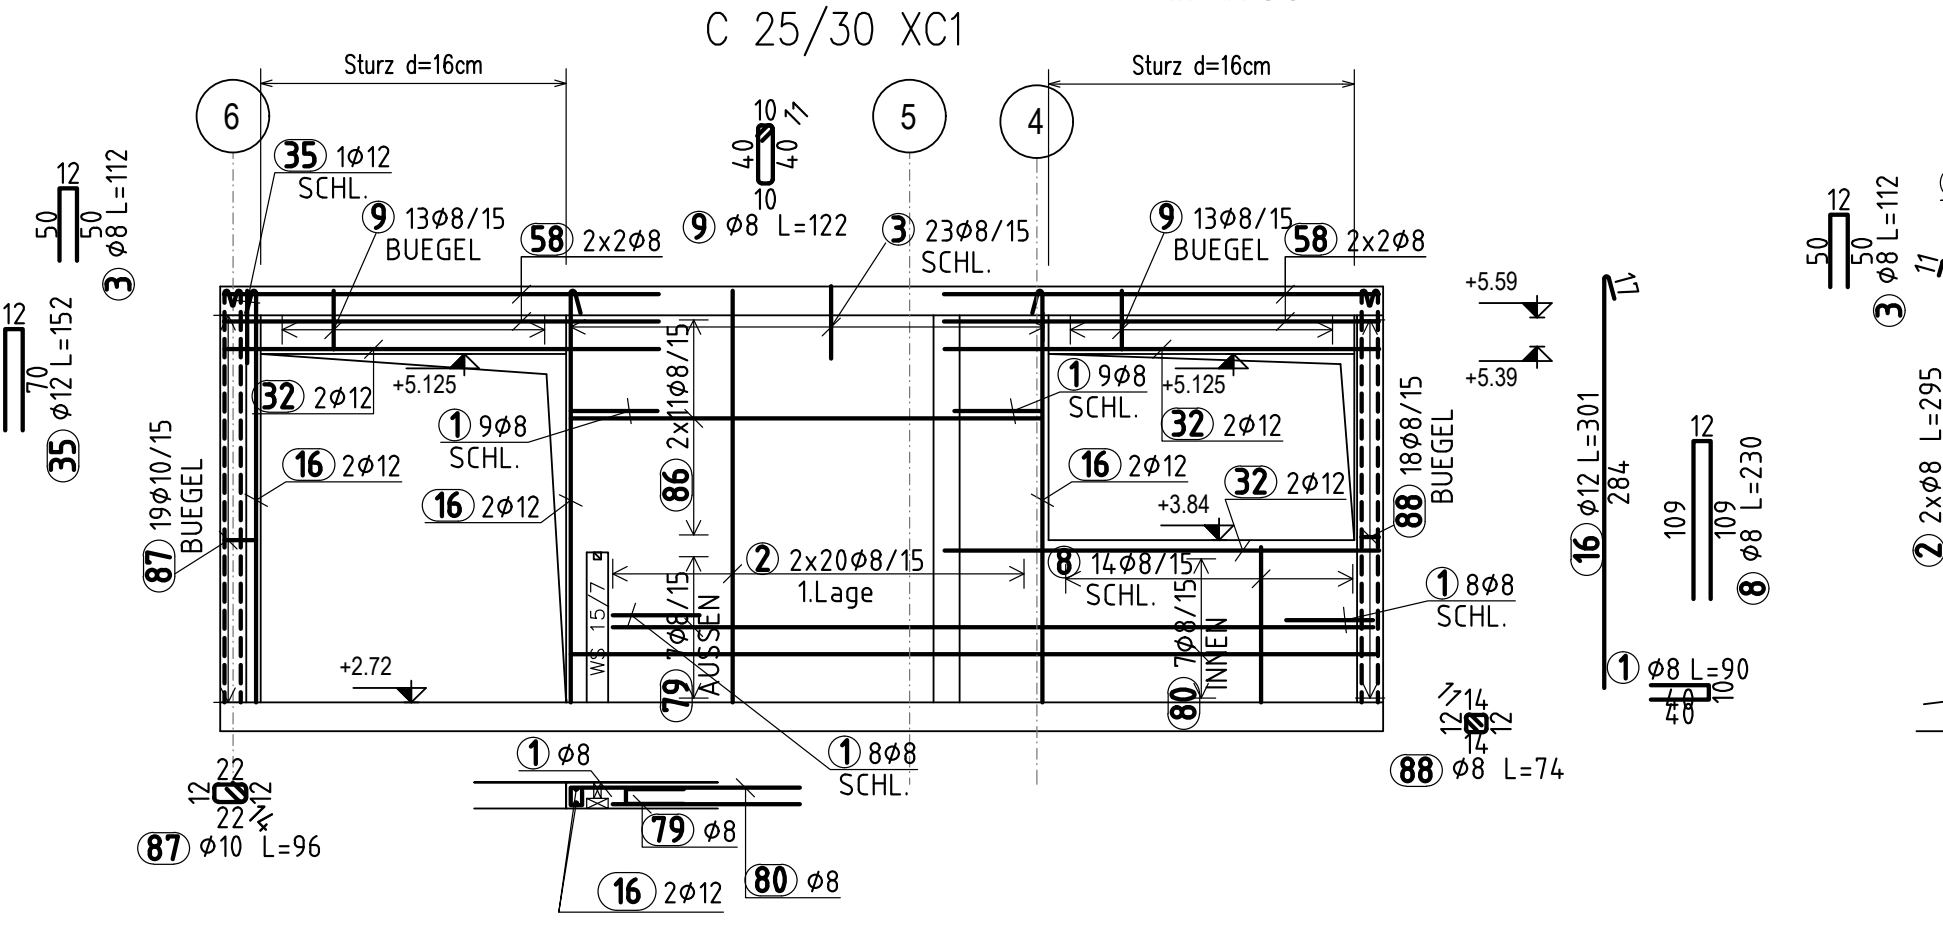

Wand 12

d=18cm M 1:50
C 25/30 XC1

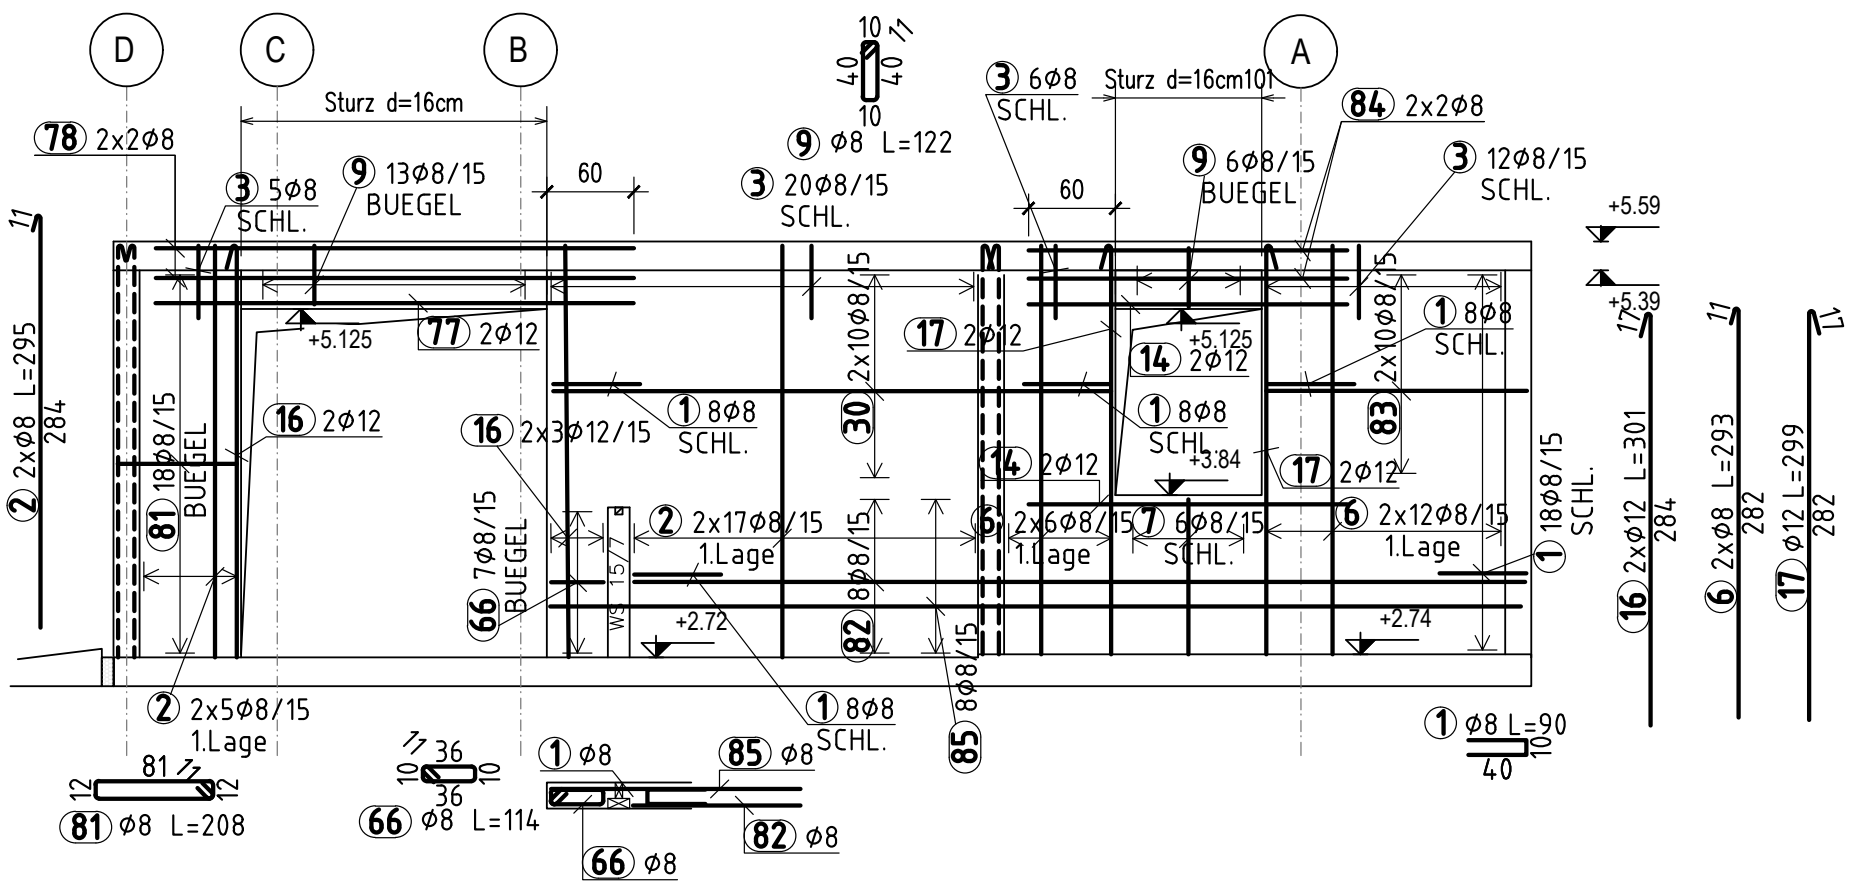

Wand 13

d=18cm M 1:50
C 25/30 XC1

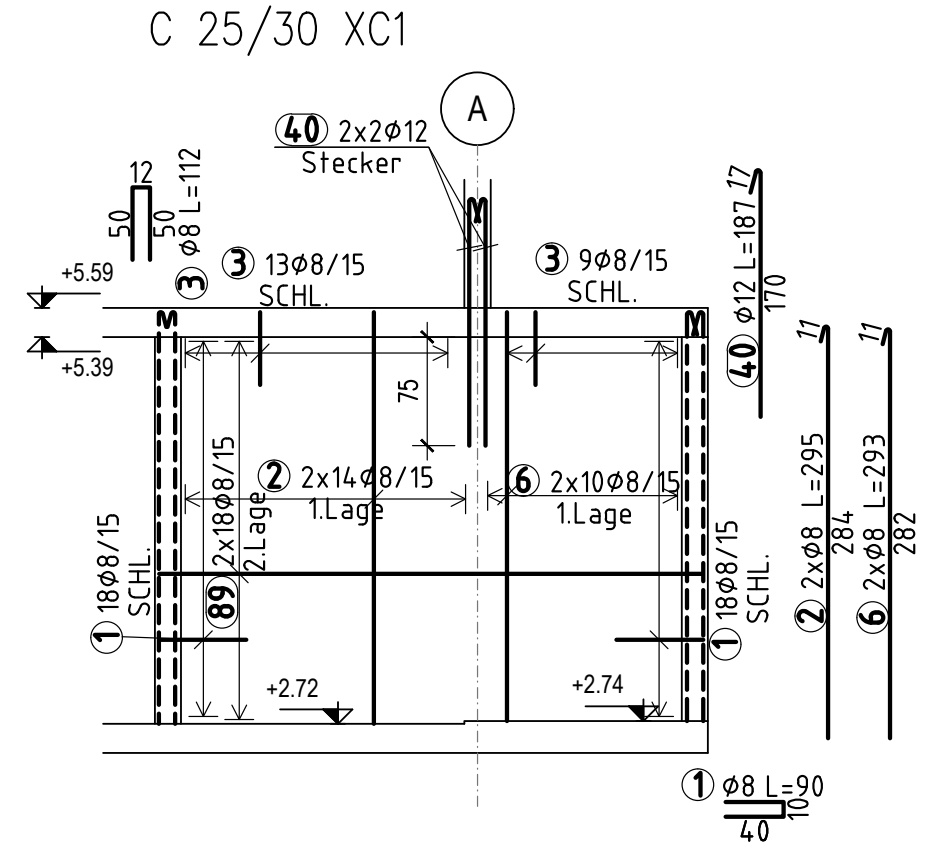

Wand 14

d=18cm M 1:50
C 25/30 XC1

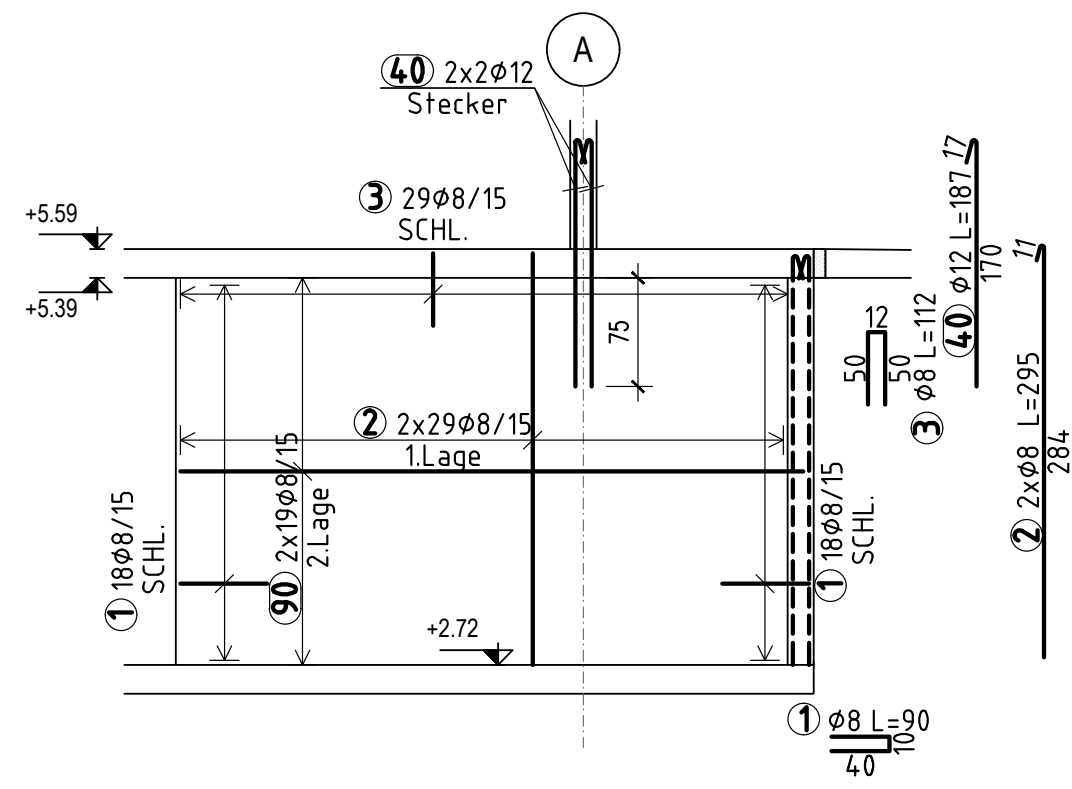

Wand 15

d=18cm M 1:50
C 25/30 XC1

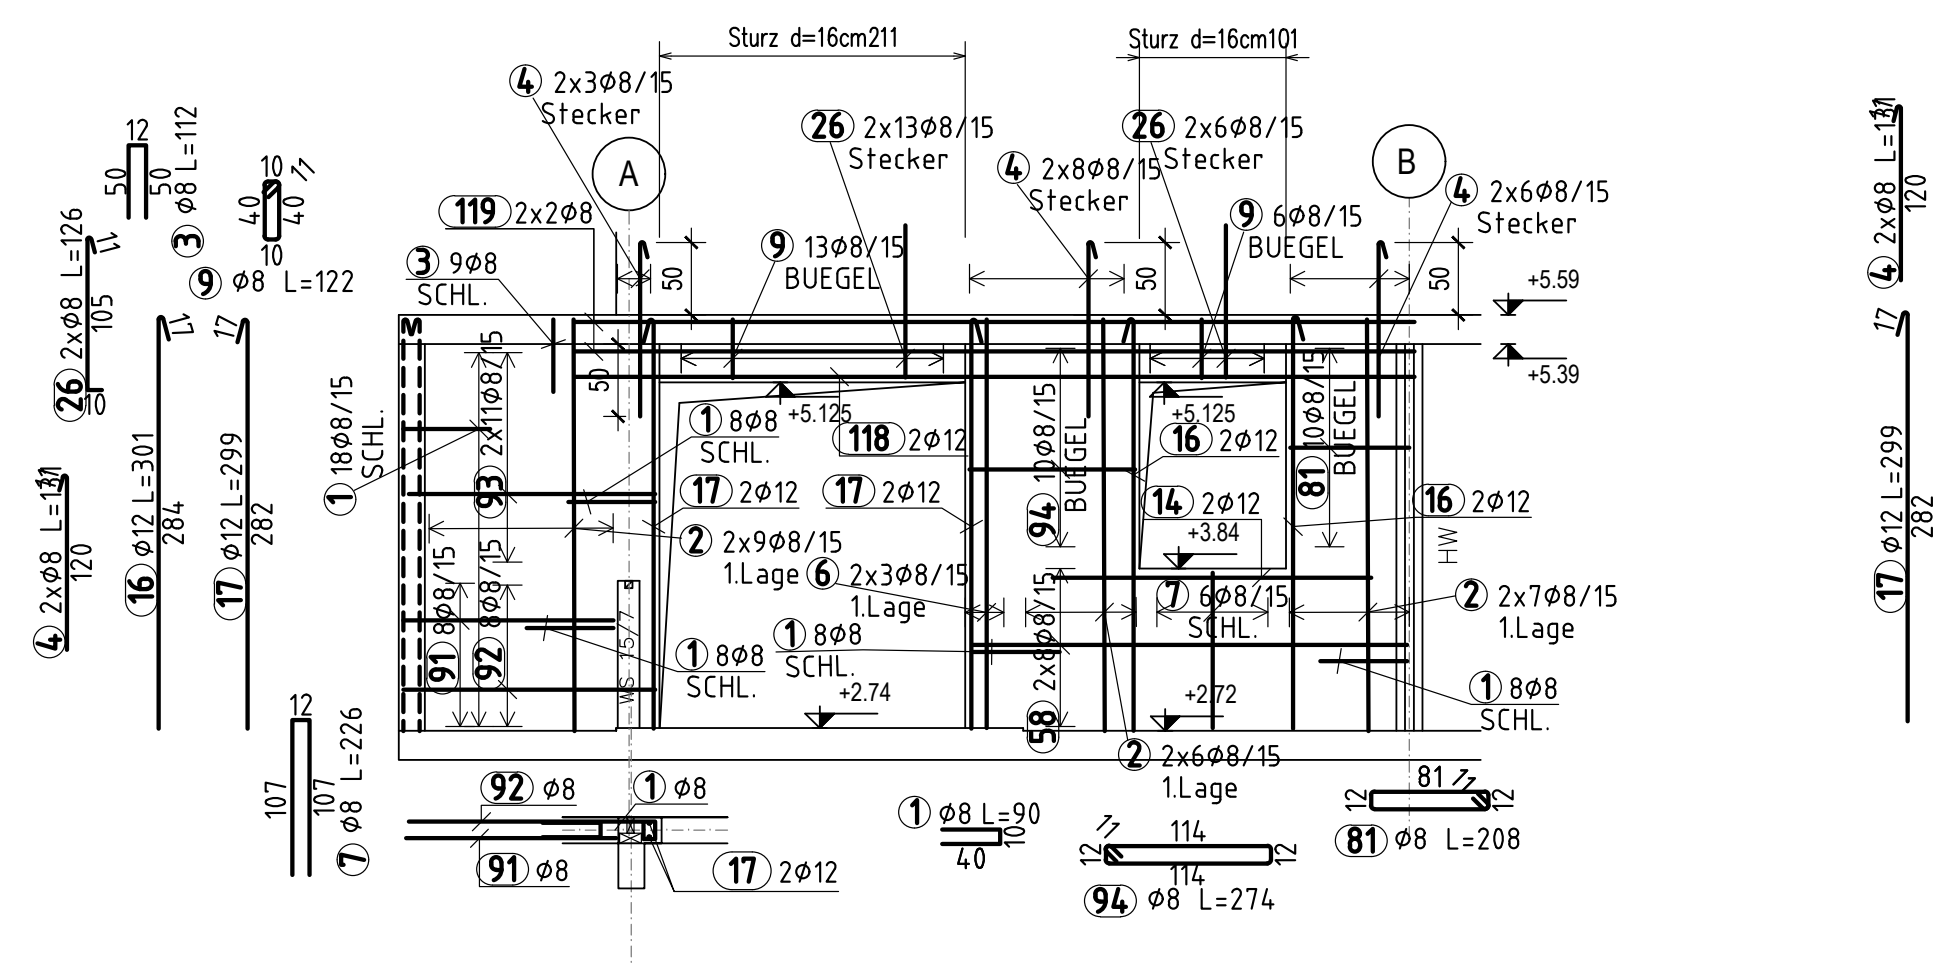

Wand 16

d=18cm M 1:50
C 25/30 XC1

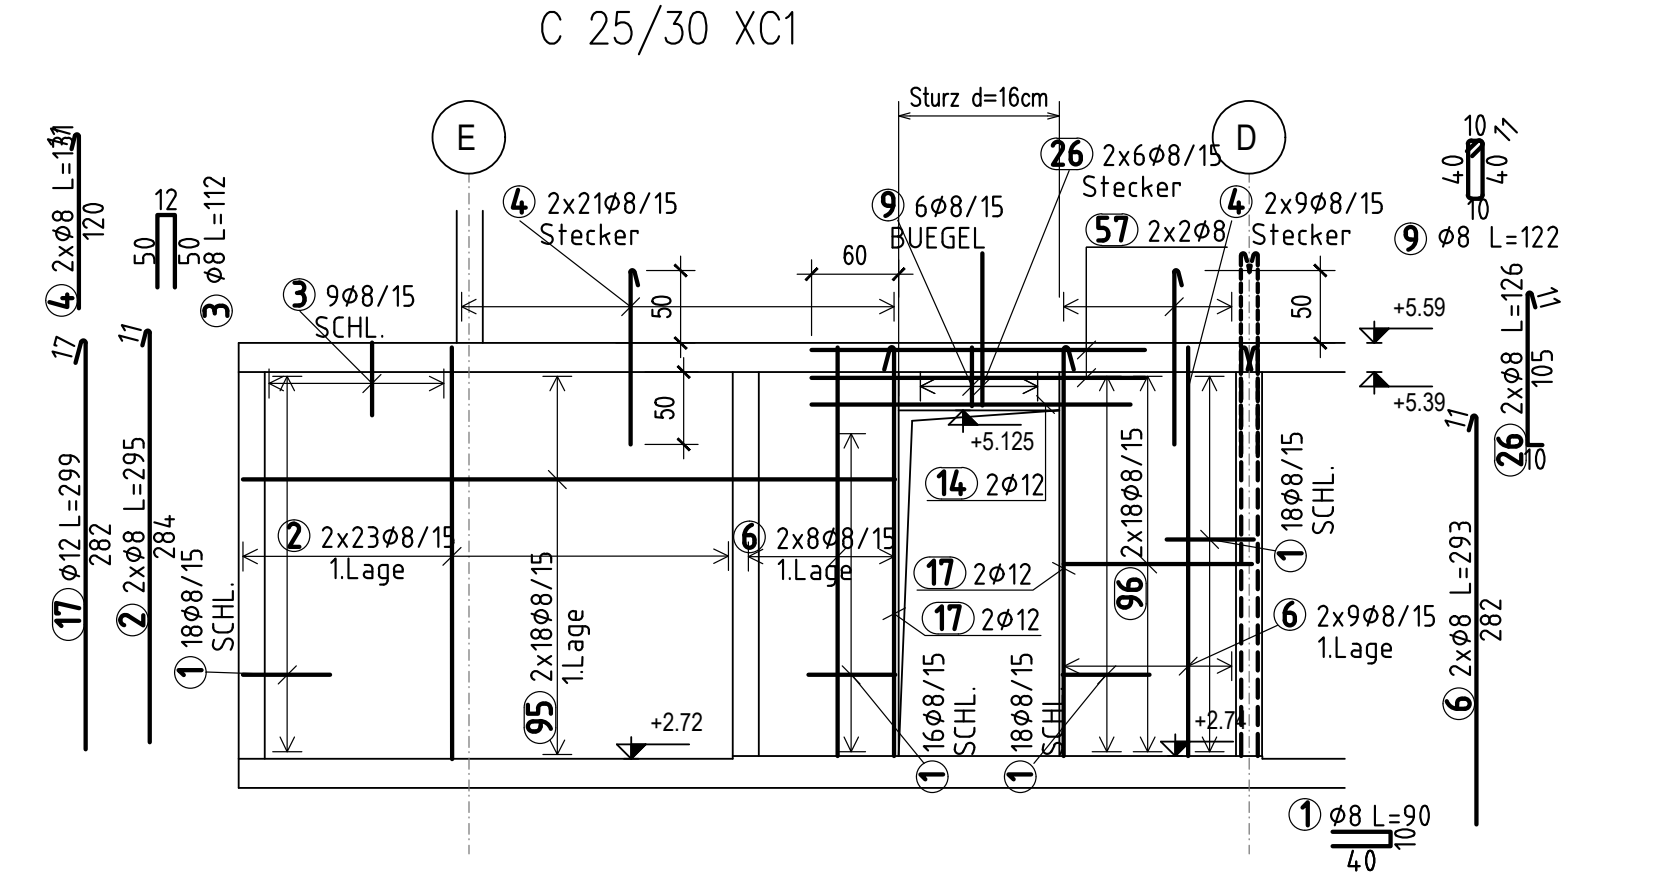

Wand 17

d=18cm M 1:50
C 25/30 XC1

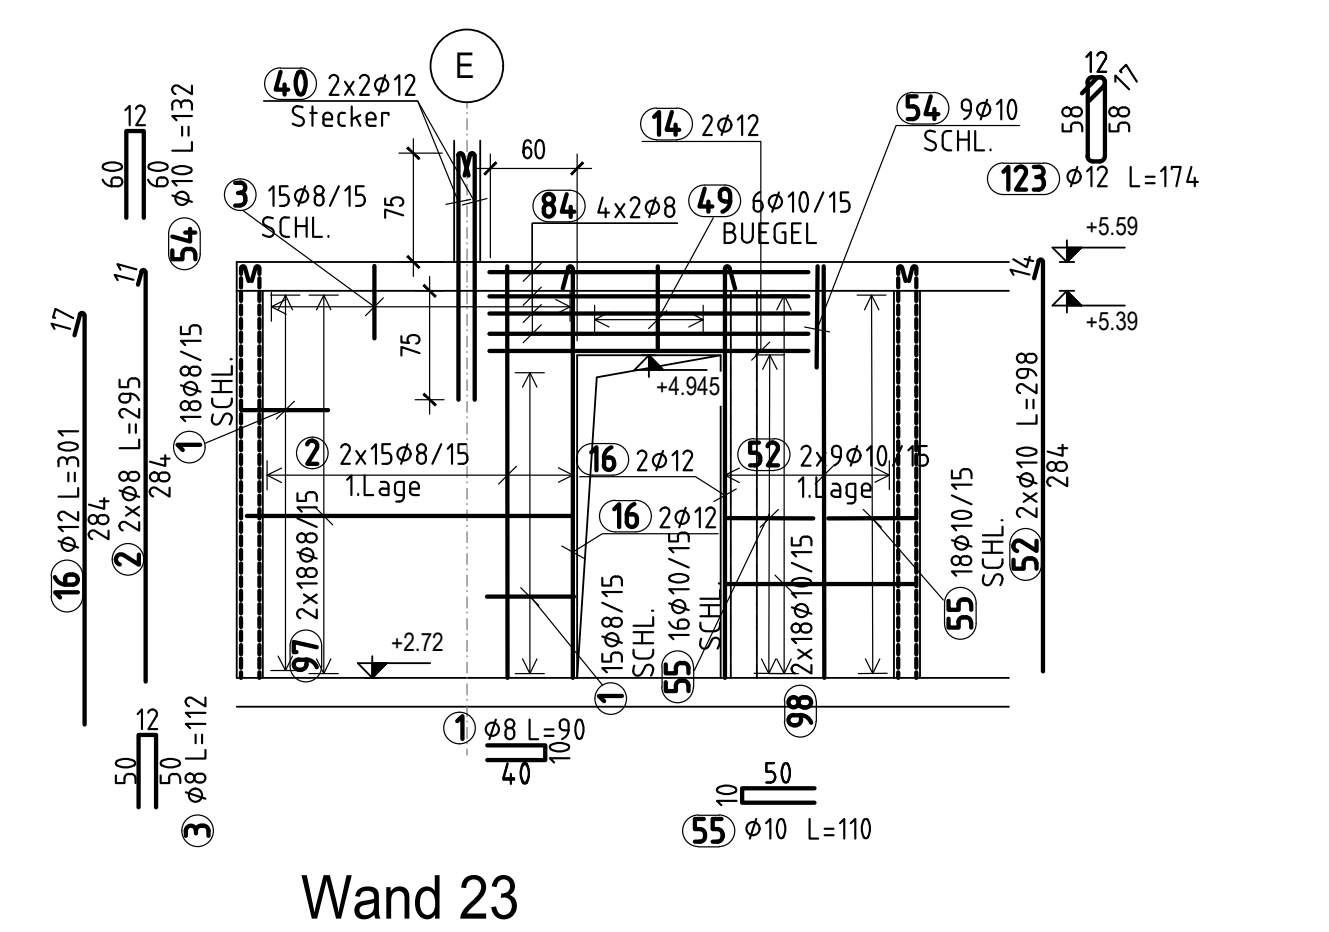

Wand 18

d=18cm M 1:50
C 25/30 XC1

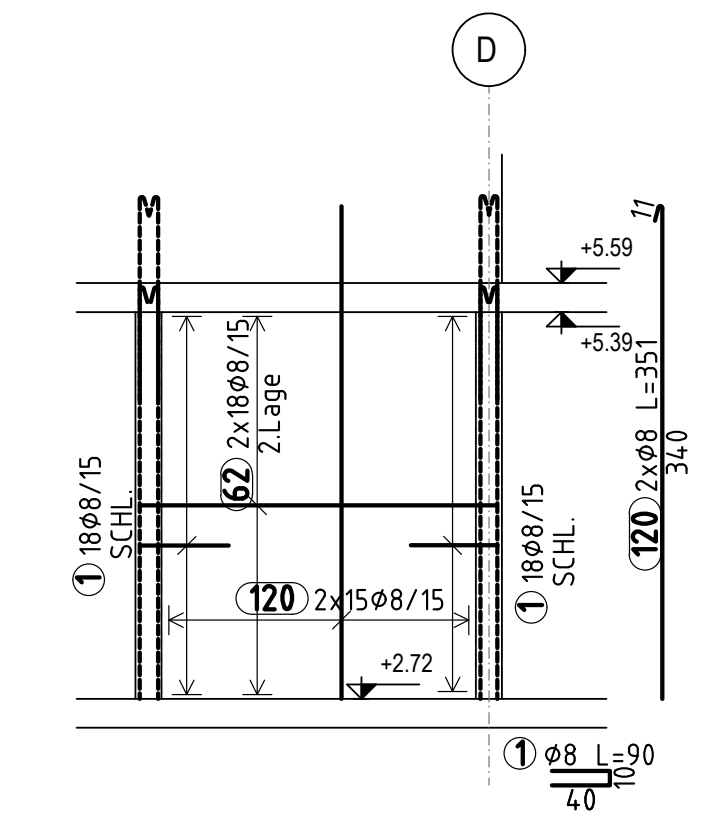

Wand 19

d=18cm M 1:50
C 25/30 XC1

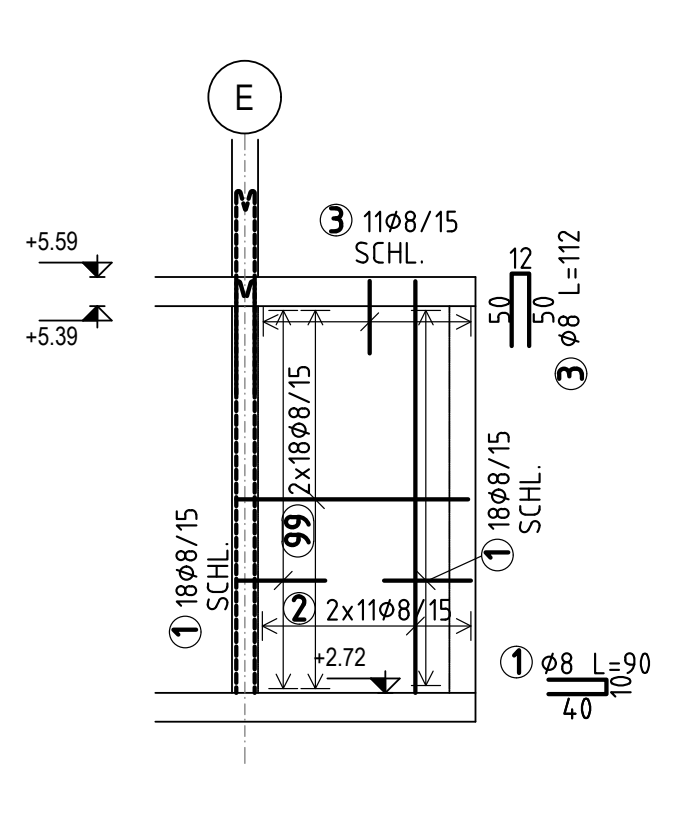

Wand 20

d=18cm M 1:50
C 25/30 XC1

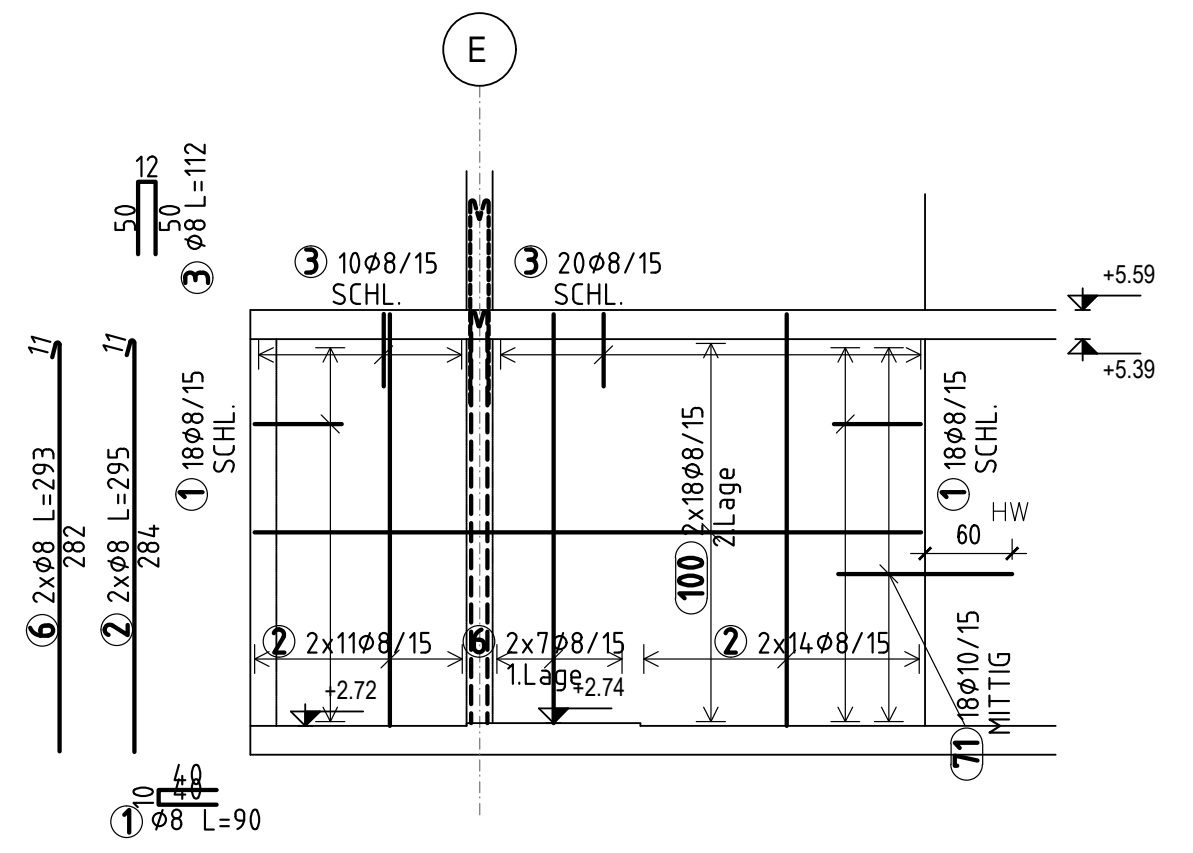

Wand 21

d=18cm M 1:50
C 25/30 XC1

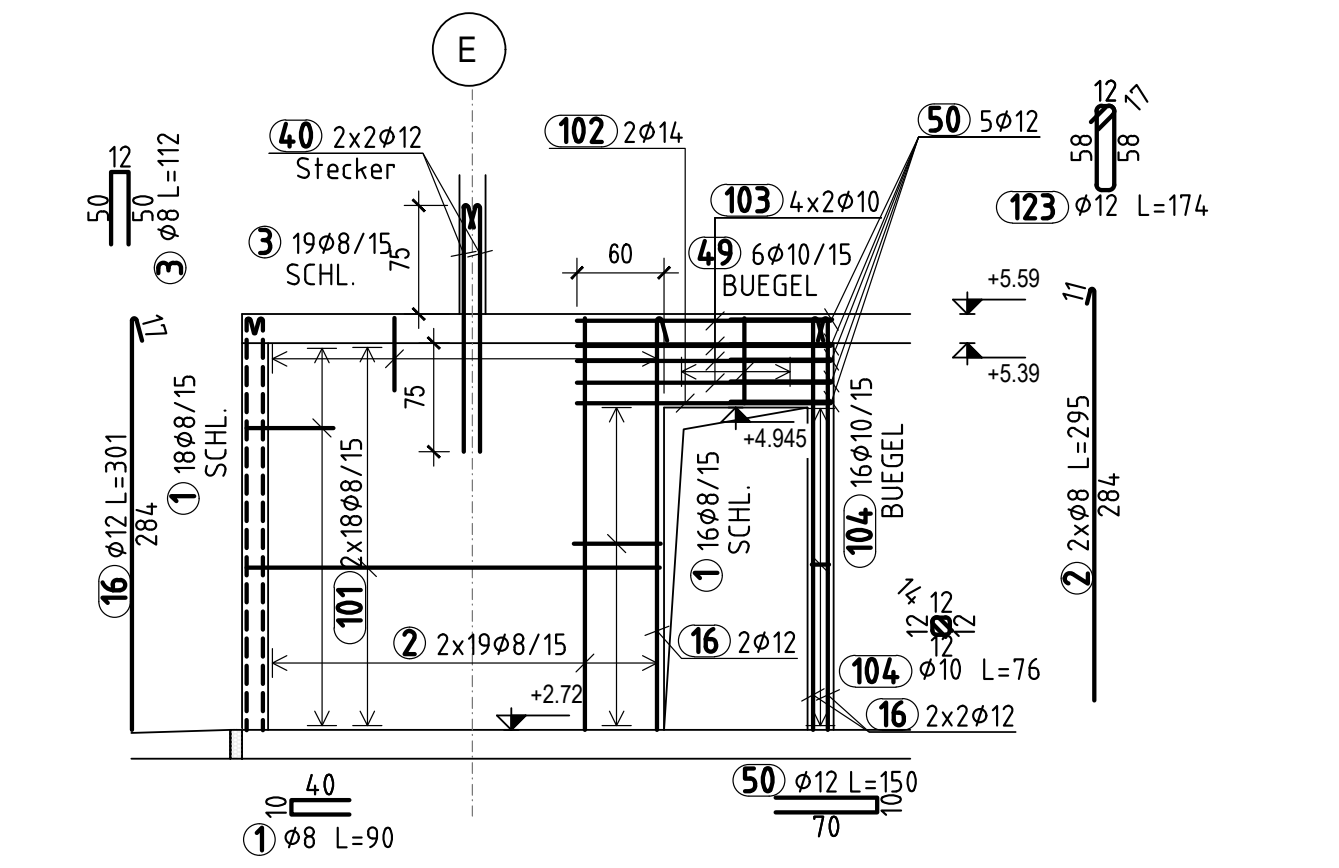

Wand 22

d=18cm M 1:50
C 25/30 XC1

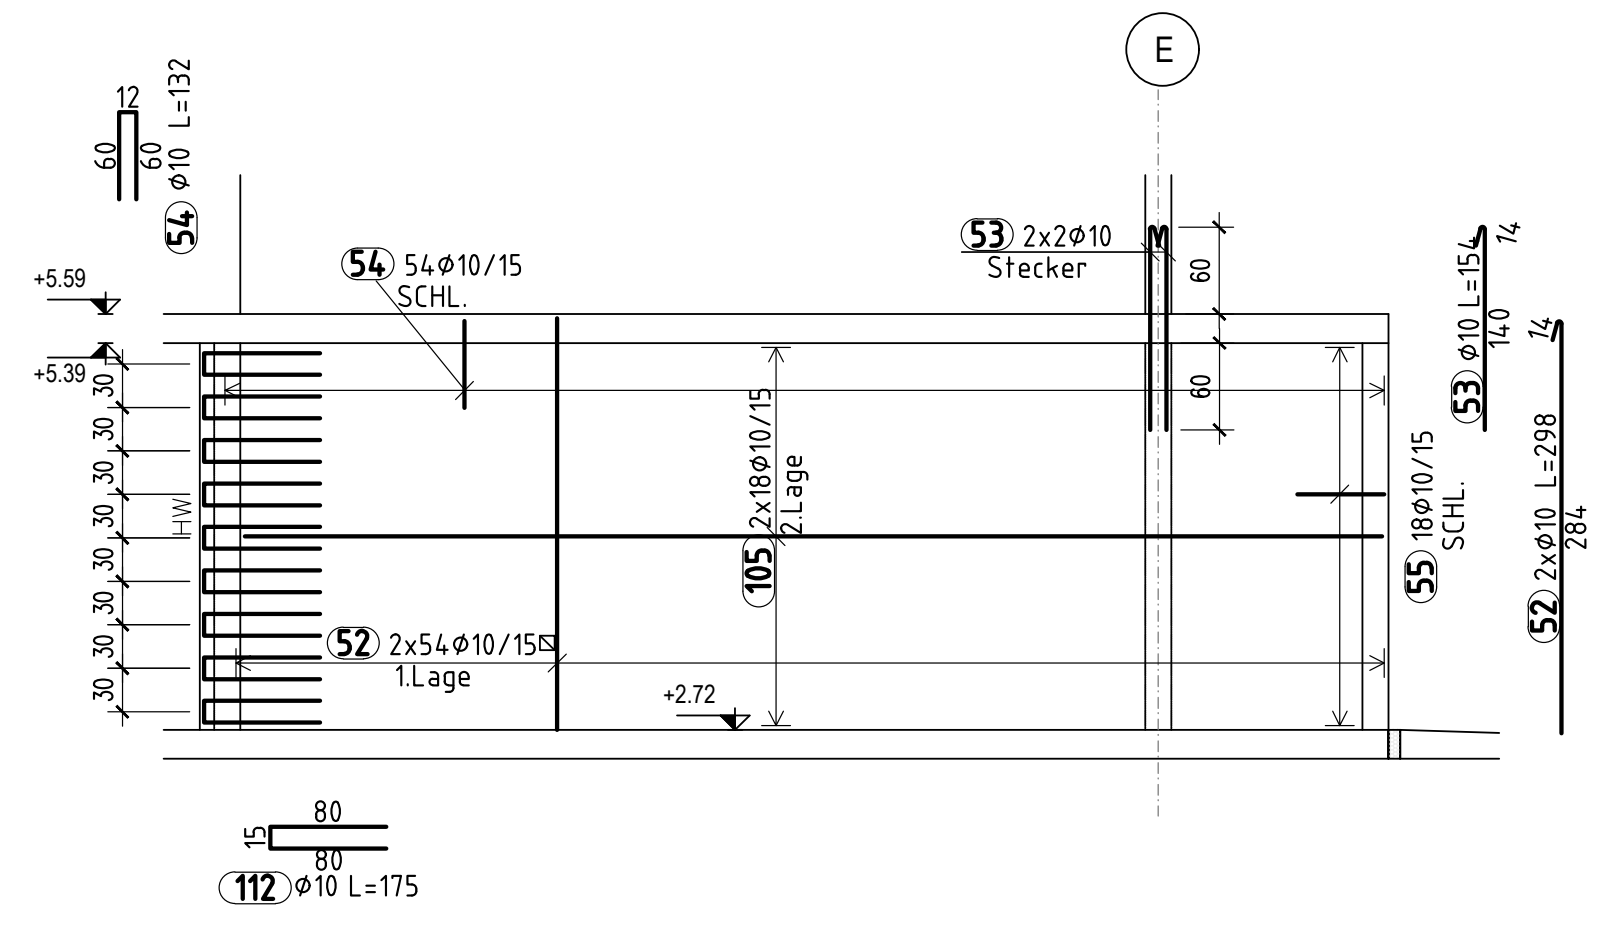

Wand 23

d=18cm M 1:50
C 25/30 XC1

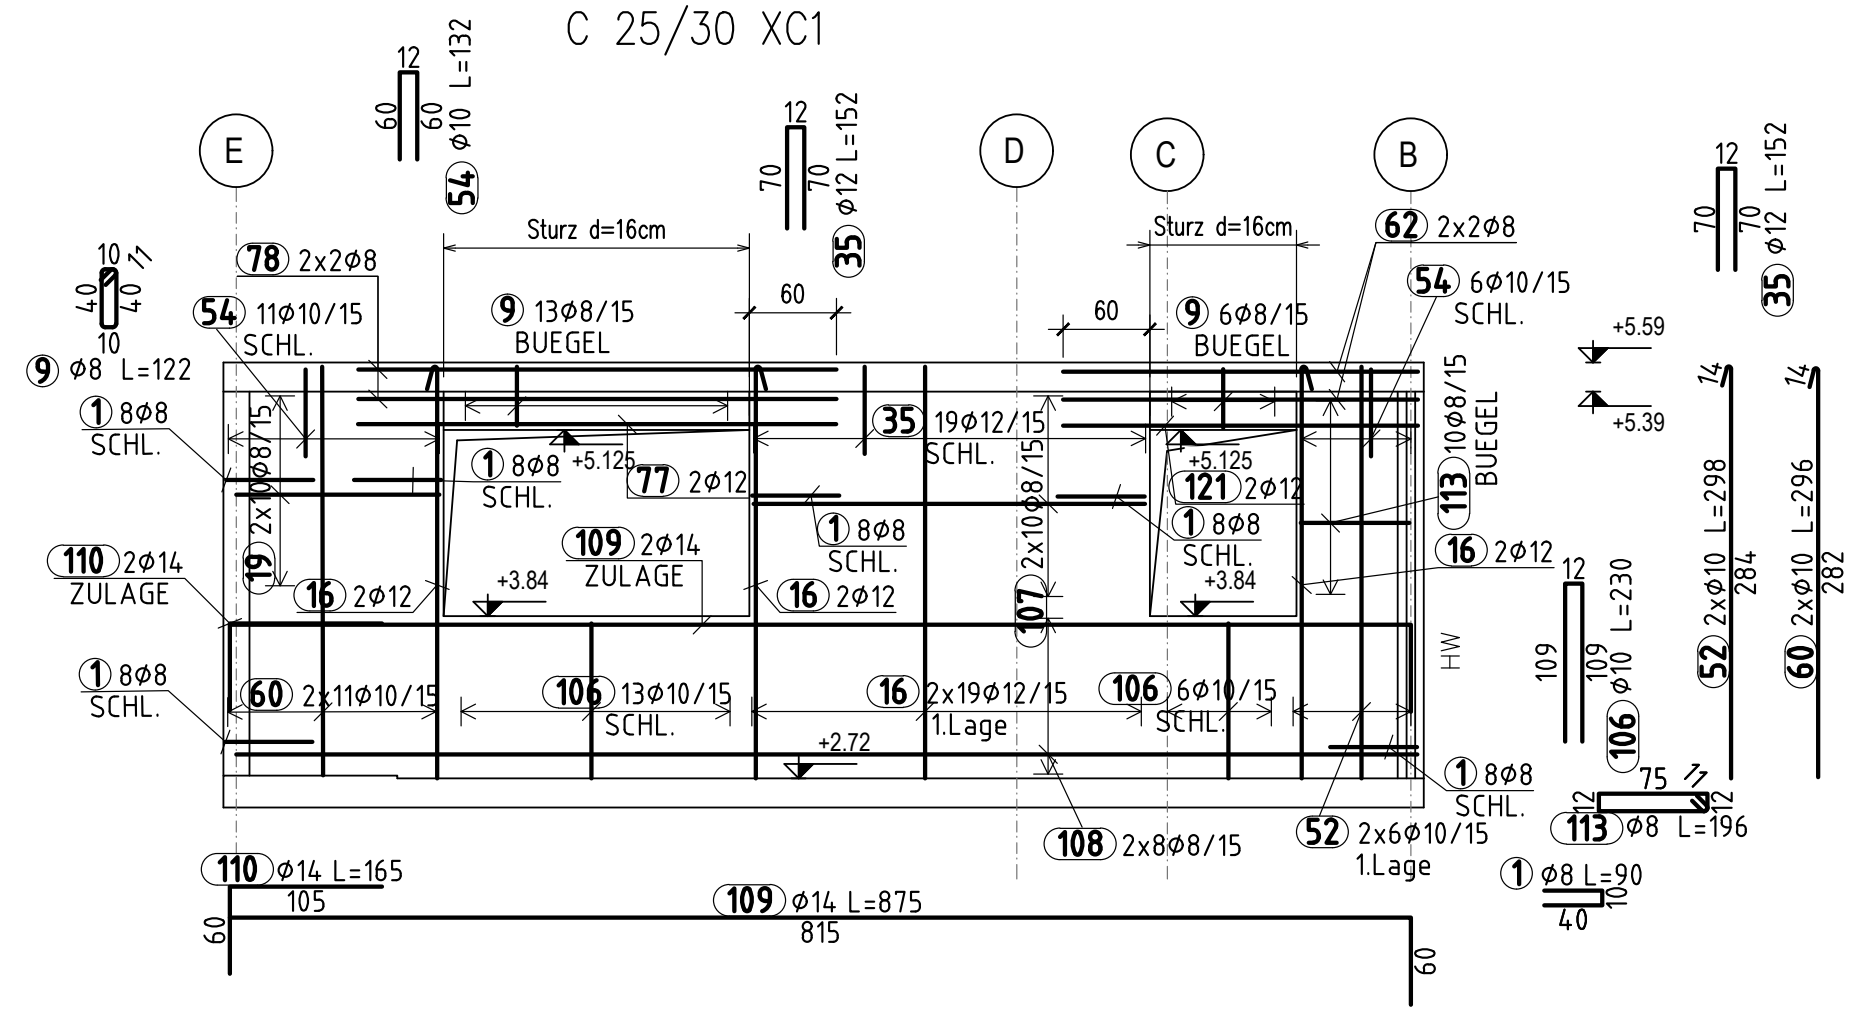

UBERSICHT

M 1:100

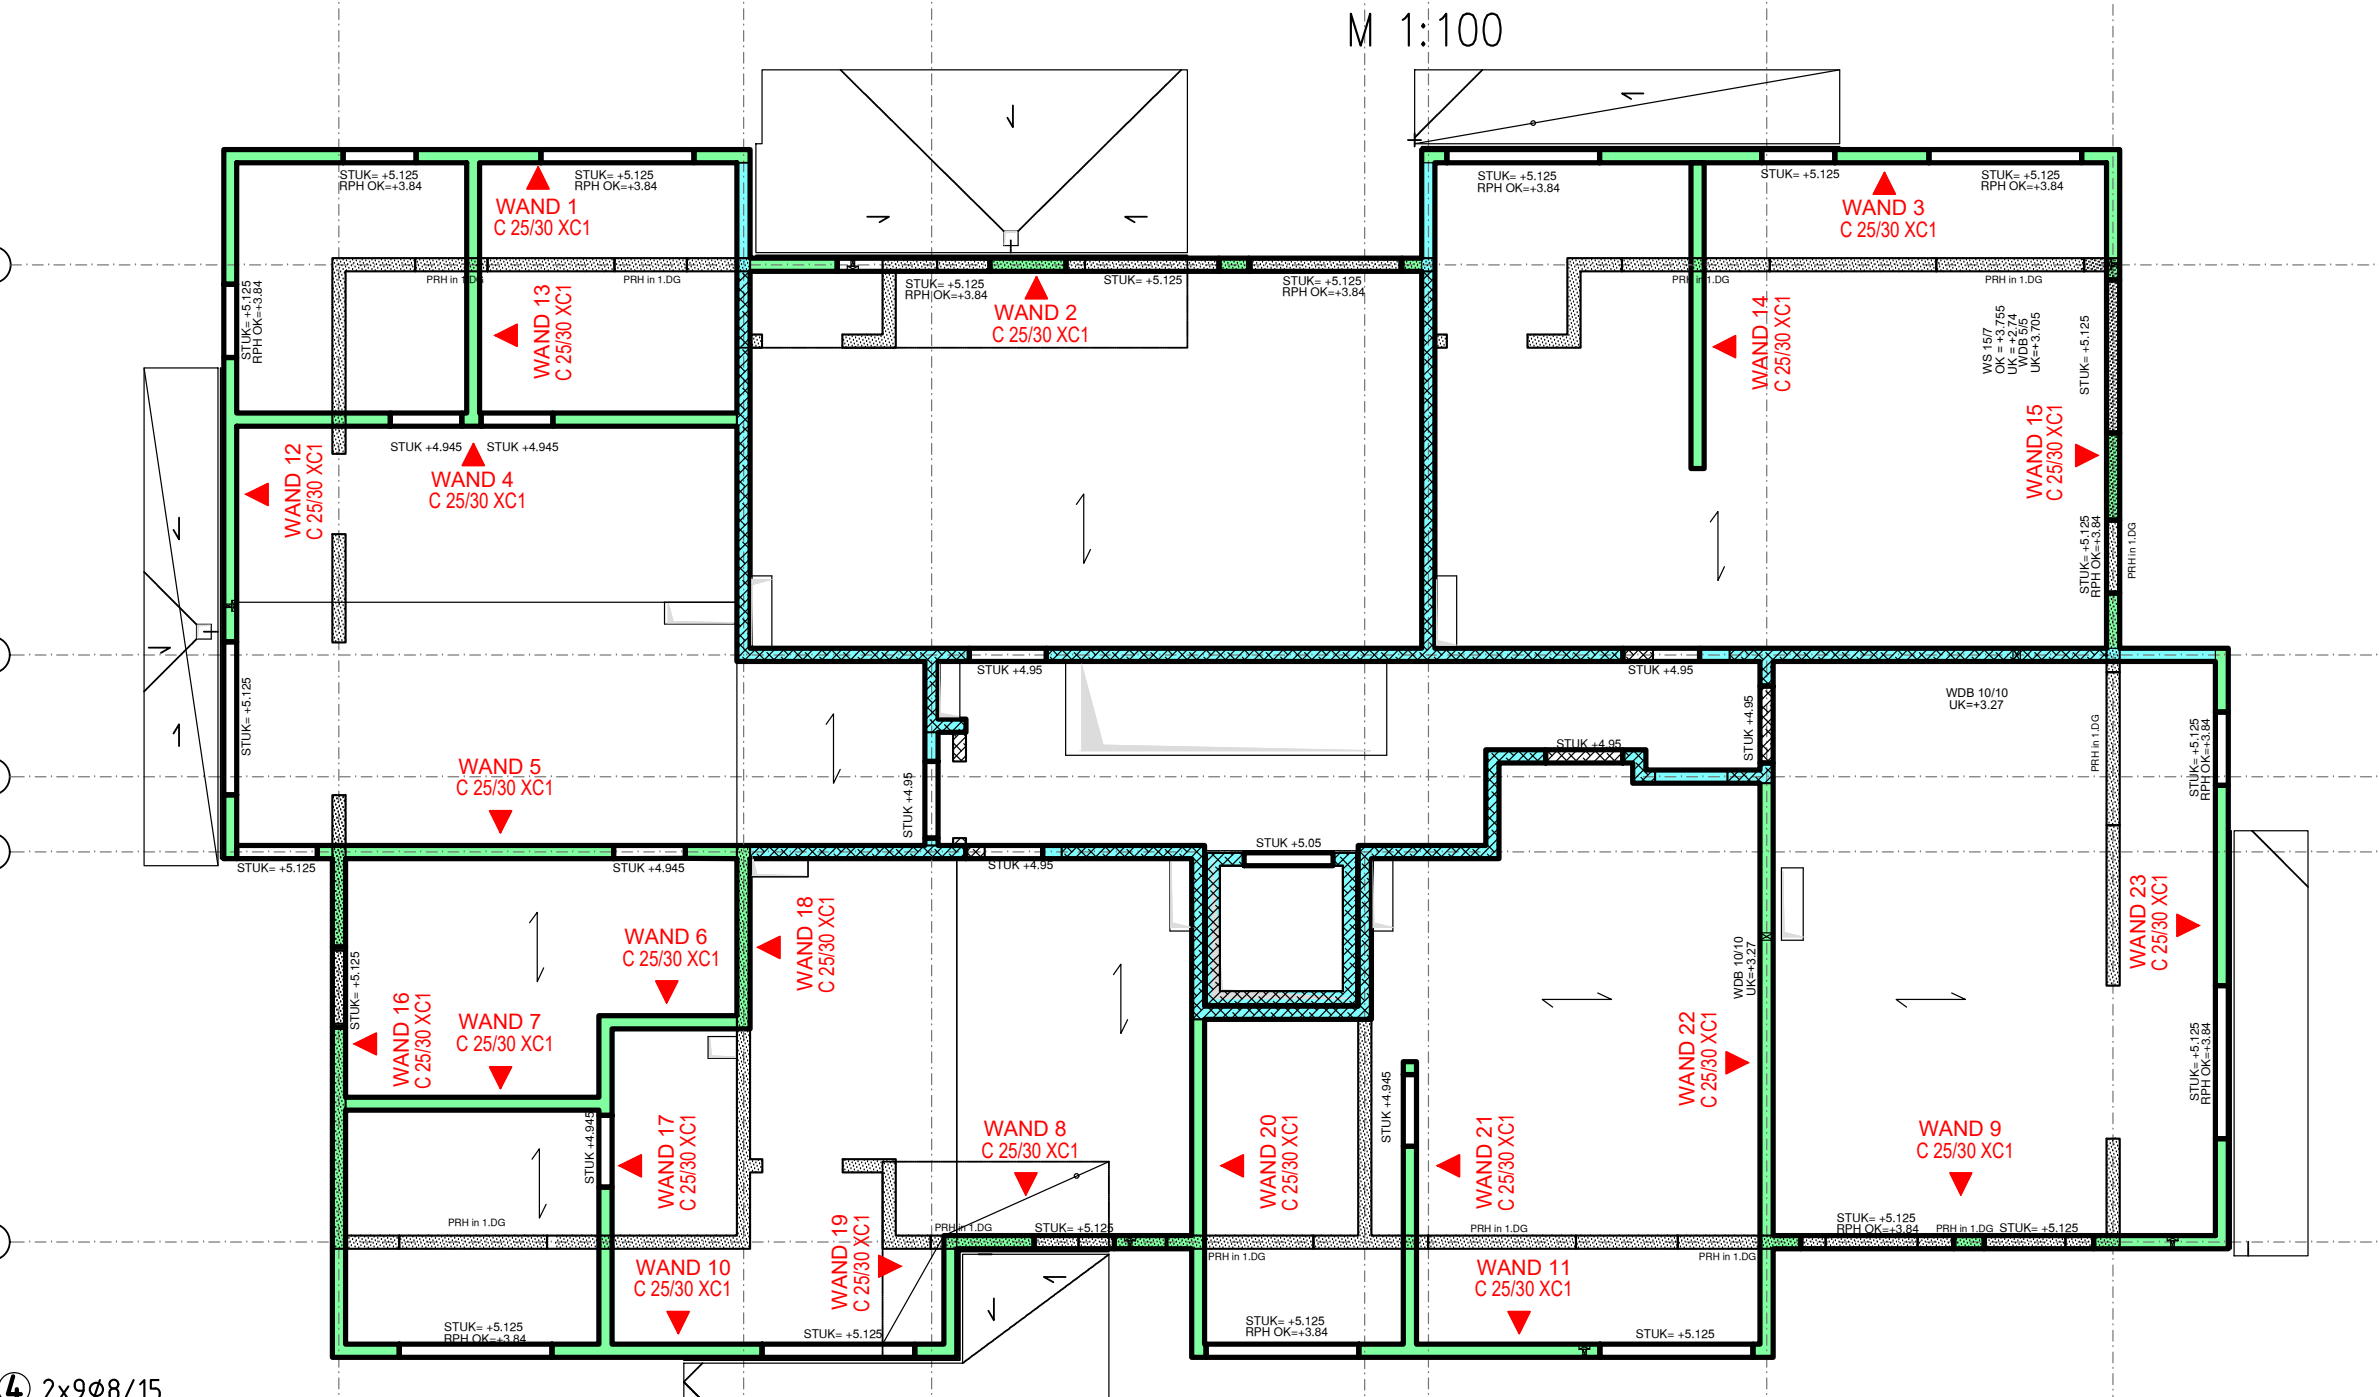

S-HAKEN

Für D=18cm.

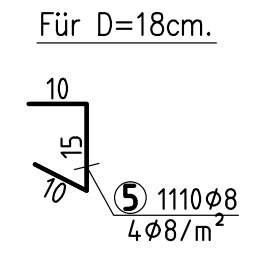

BETON

Betonfestigkeitsklasse: C25/30
Expositionsklasse: XC1

Vom Planverfasser werden die Betonfestigkeitsklasse sowie die Expositionsklasse gemäß ÖNORM B4710–1 vorgegeben. Es gelten die landesspezifischen Regelungen für Österreich (A).
Die sonstigen Betoneigenschaften sind vom Besteller entsprechend den jeweiligen Anforderungen festzulegen.
Für Verarbeitung und Nachbehandlung sind die Anforderungen der ÖNORM B4710–1 einzuhalten.

BETONDECKUNG: c=3,0cm

DETAIL AUFBIEGUNGEN

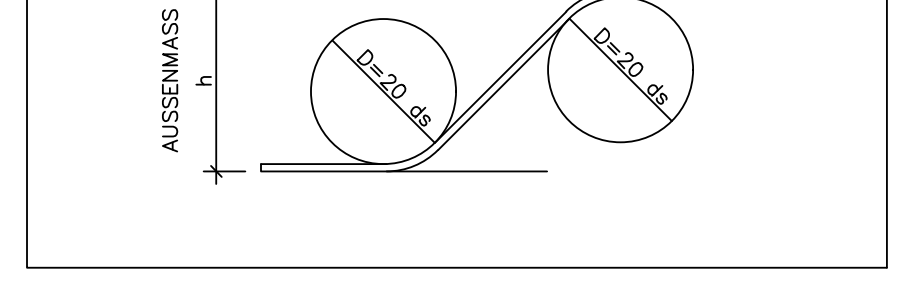

BEWEHRUNGSSTAHL

Stabstahl:	BSt550A
Mattenstahl:	BSt550M

Mindestbiegerollendurchmesser

Stabdurchmesser	Ø m, min
Ø ≤ 16mm	4 Ø
Ø > 16mm	7 Ø

Die Bemaßung der Biegeformen erfolgt gemäß ÖNORM A6220 bzw. ÖNORM ISO 3766.
Die angegebenen Maße sind wenn nicht anders angegeben Außenabmessungen.

UNFALLSCHUTZ

Gerade nach oben endene Stäbe (Steckeisen) müssen abgedeckt oder zusätzlich hakenförmig abgebogen werden. Dies hat ohne Verringerung der Haftlänge zu erfolgen.

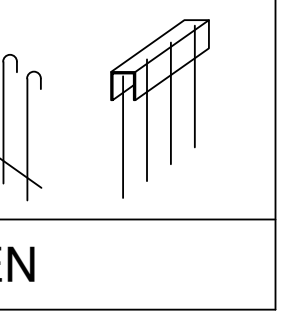

NATURMASSE NEHMEN

INDEX	DATUM	GEZ.	GEPR.	ÄNDERUNGEN
A04				
A03				
A02				
A01				

PROJEKT: NEUBAU EINER WOHNHAUSANLAGE
UND REIHENHÄUSER MIT TIEFGARAGE
1220 Wien, Am Freihof 7-9

GRST.NR.: 39/1
EZ.: 1184
KAT.GEM.: Kagran (01660)

PLANVERFASSER:

TRIAX ZT GmbH
ZIVILTECHNIKER GmbH
1100 Wien Columbusplatz 7-8/3/4 www.triax-zt.at
T: +43(1)6652830 F: +43(1)6652830-36 E: wien@triax-zt.at
4020 Linz Herrenstrasse 5/1 www.triax-zt.at
T: +43(732)771777-0 F: +43(732)771777-10 E: linz@triax-zt.at

BAUHERR:

3SI Am Freihof GmbH & Co KG
Tegetthoffstrasse 7, 1010 Wien

PLANINHALT: **Wände im 1.OG**
Bewehrung Teil 2

ZUGEHÖRIGE PLÄNE:

GEZEICHNET:	**SP**	SACHBEARBEITER:	**KM**	STATIK:	**KM**
DATUM:	**01.02.2024**	MASSSTAB:	**1:50**	FORMAT:	**84/ 180**
GZ.NR.:	**22-357**	PLANNUMMER:	**034**	INDEX:	A00

DATEINAME: **034-B-Wände im 1.OG Bewehrung Teil 2**

DIESER PLAN IST URHEBERRECHTLICH GESCHÜTZT. VERVIELFÄLTIGUNGEN SIND NUR MIT SCHRIFTLICHER GENEHMIGUNG DER GESCHÄFTSFÜHRUNG VON DER TRIAX ZIVILTECHNIKER GmbH GESTATTET.