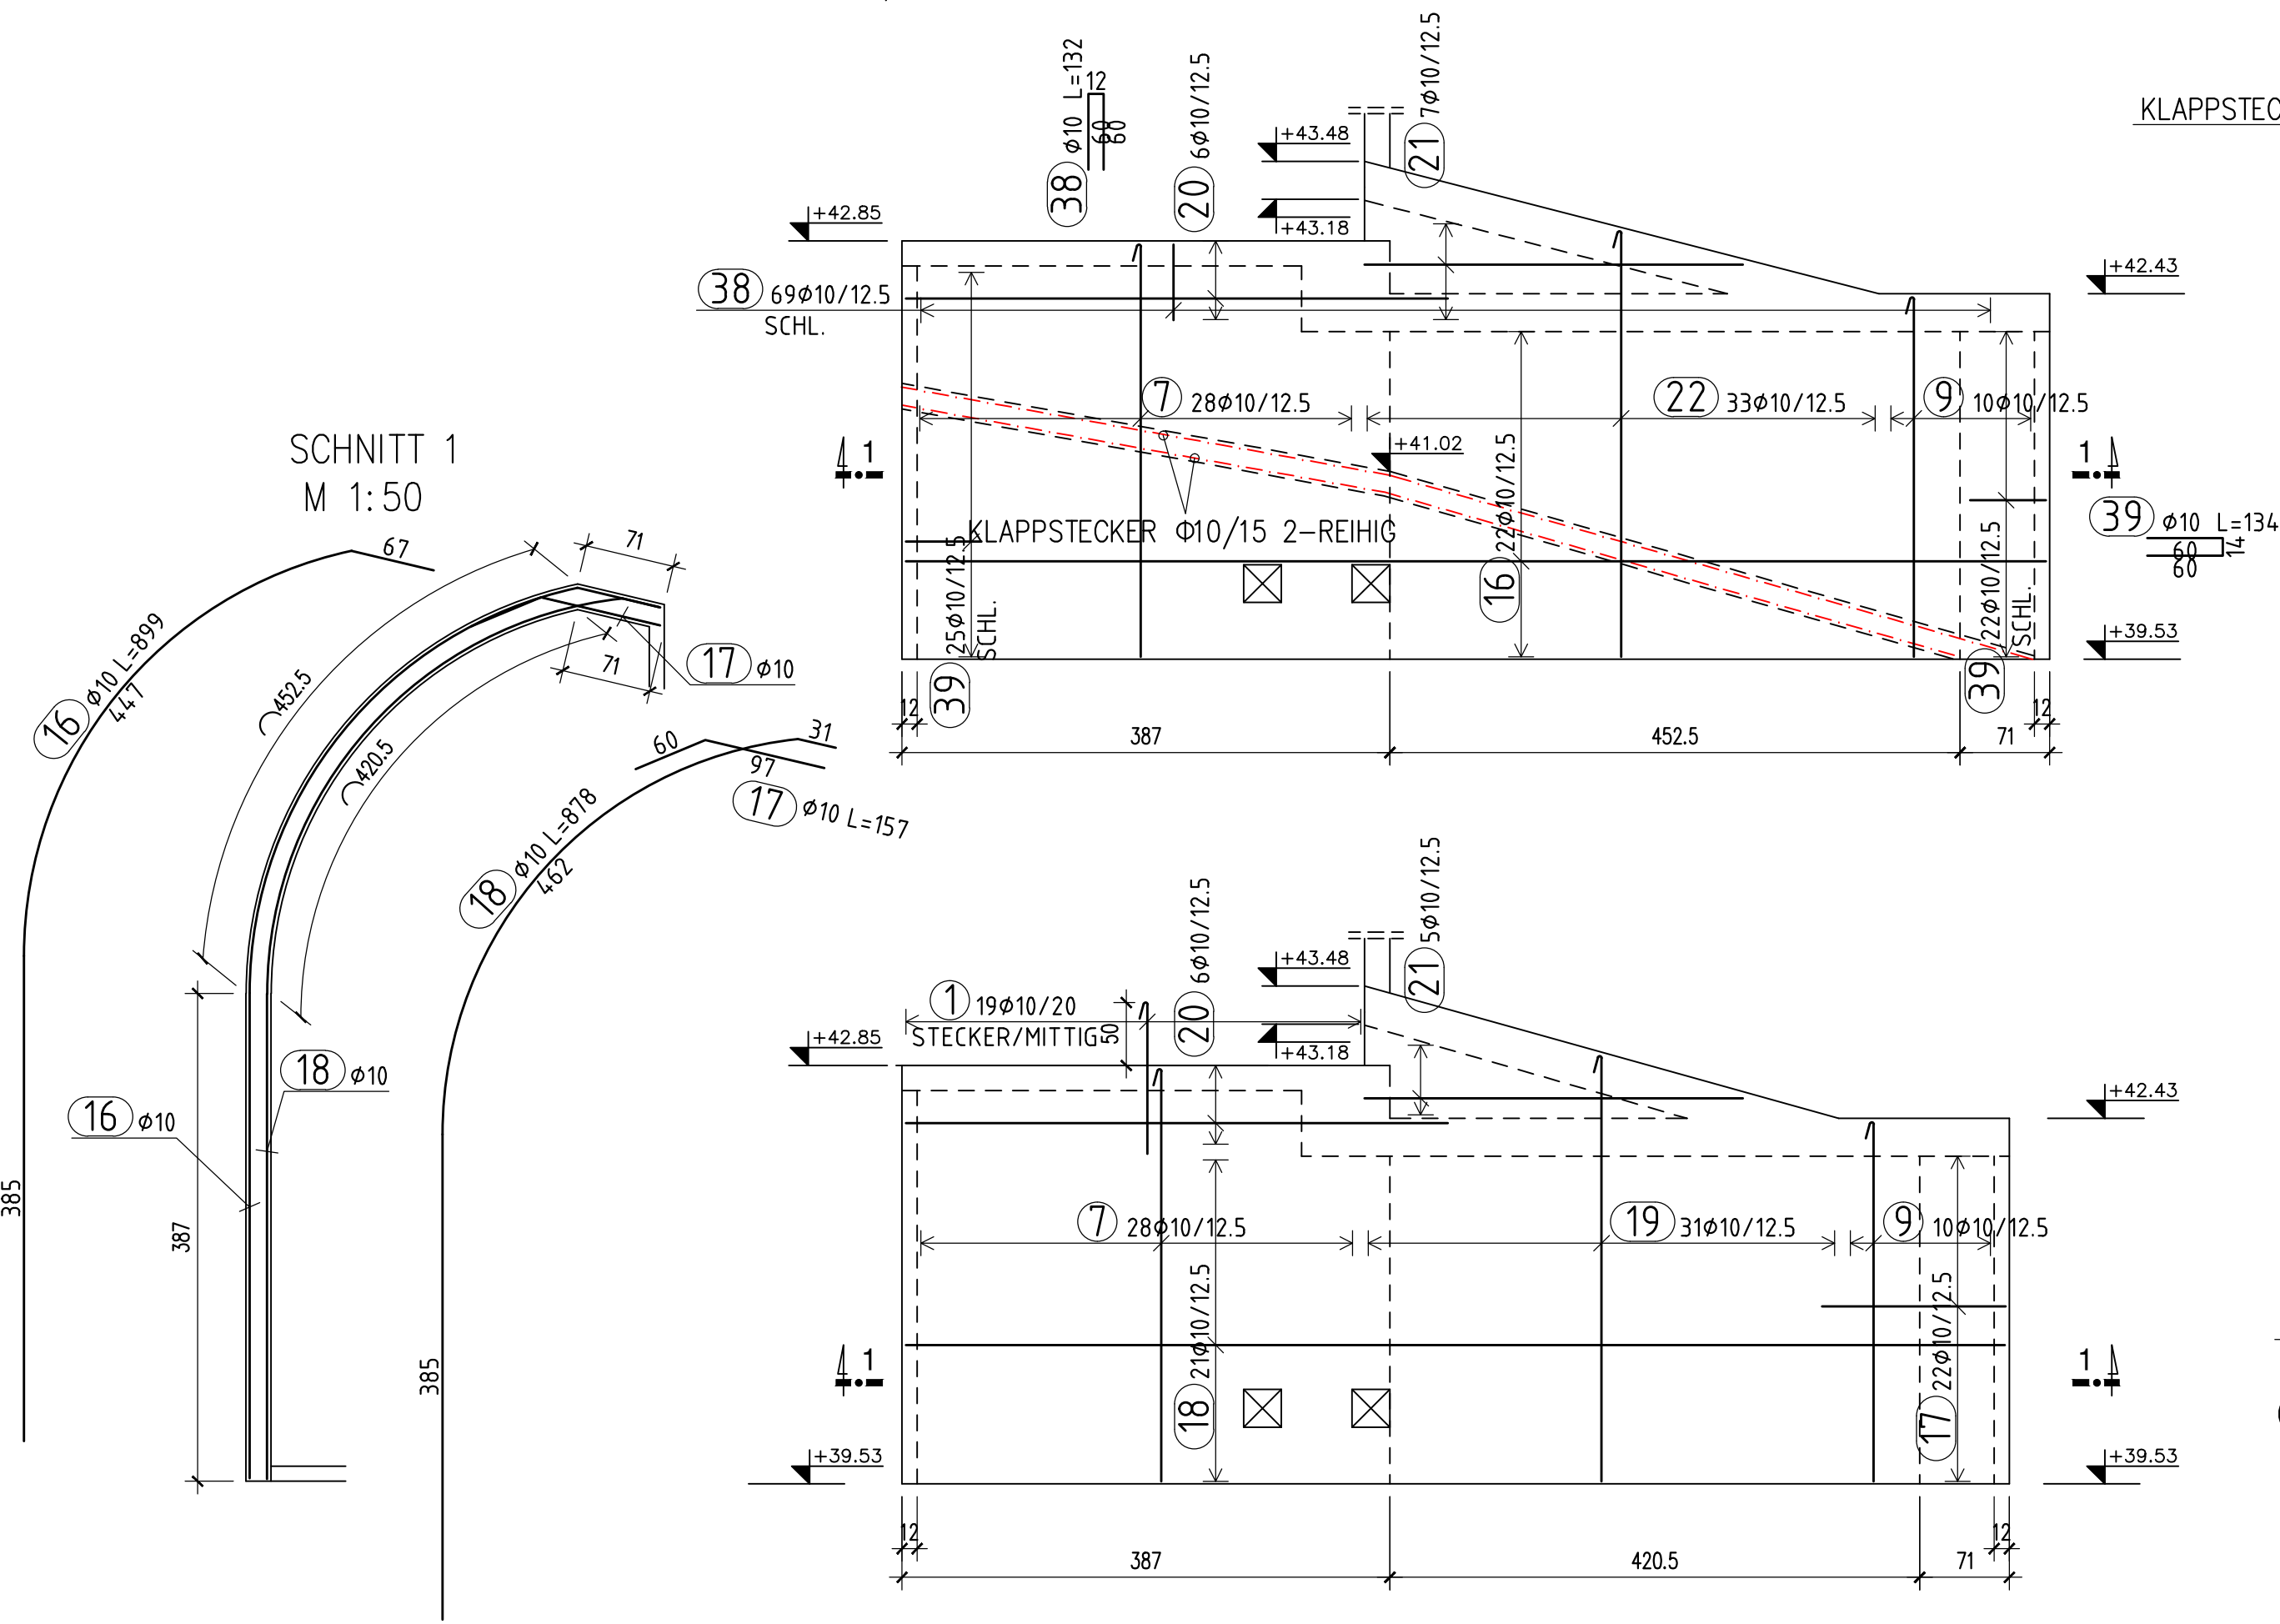
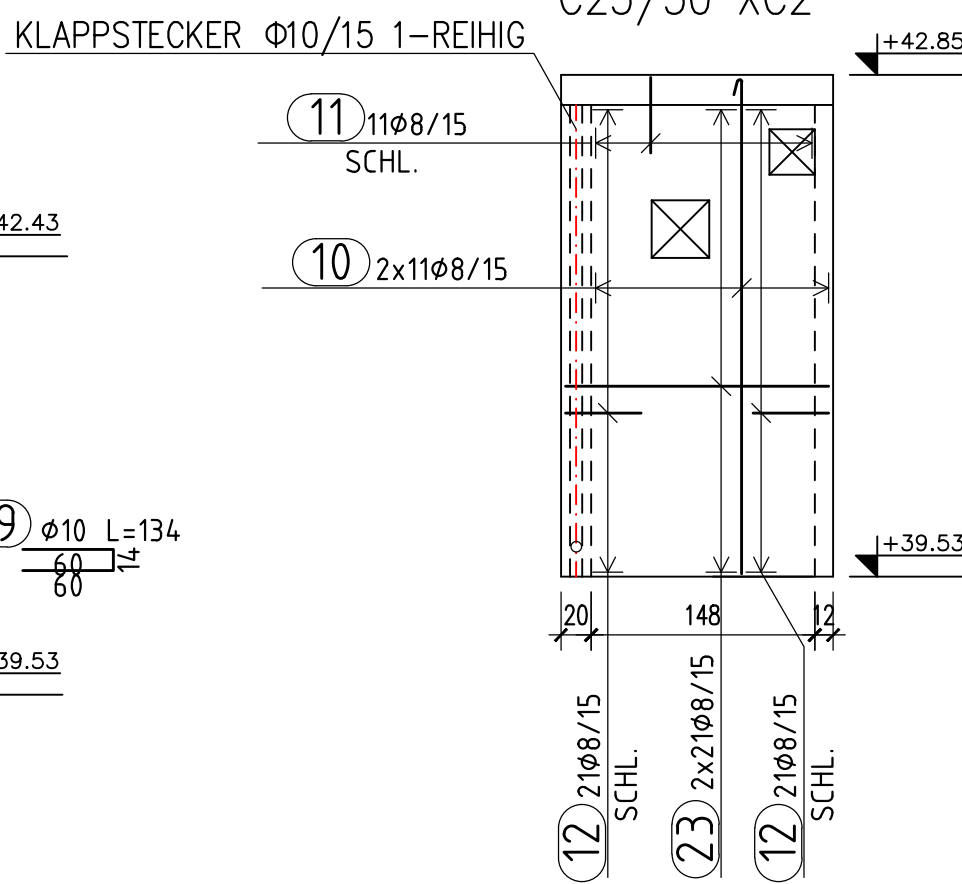


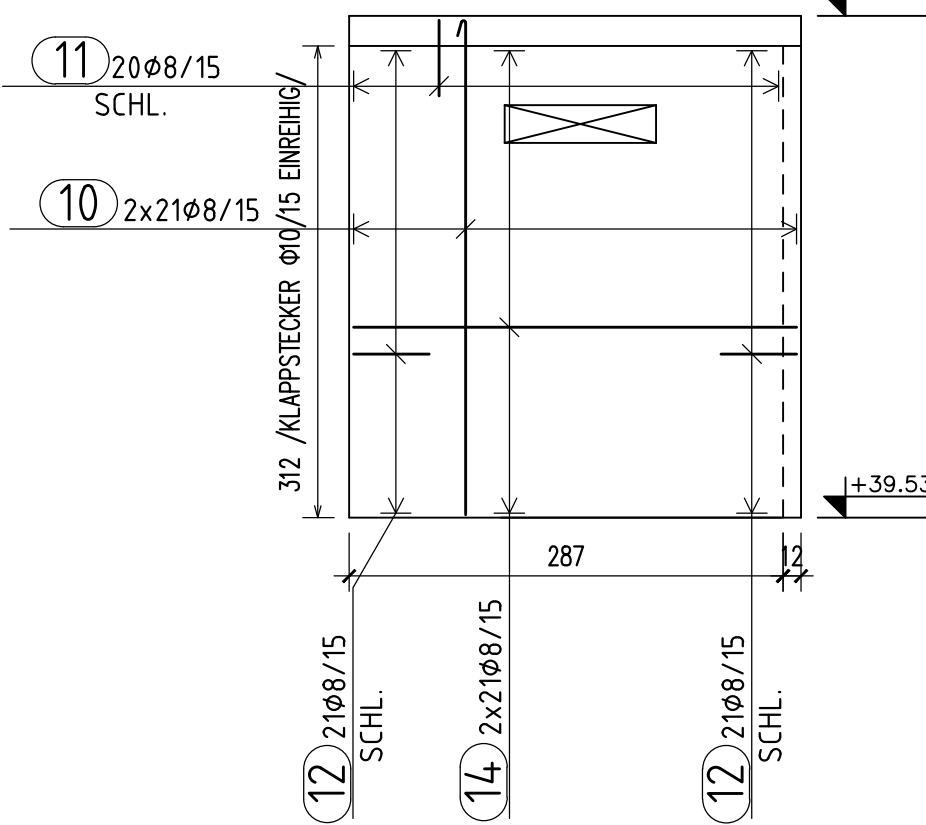
Wand B-1

d=20cm
C25/30 B2 M 1:50

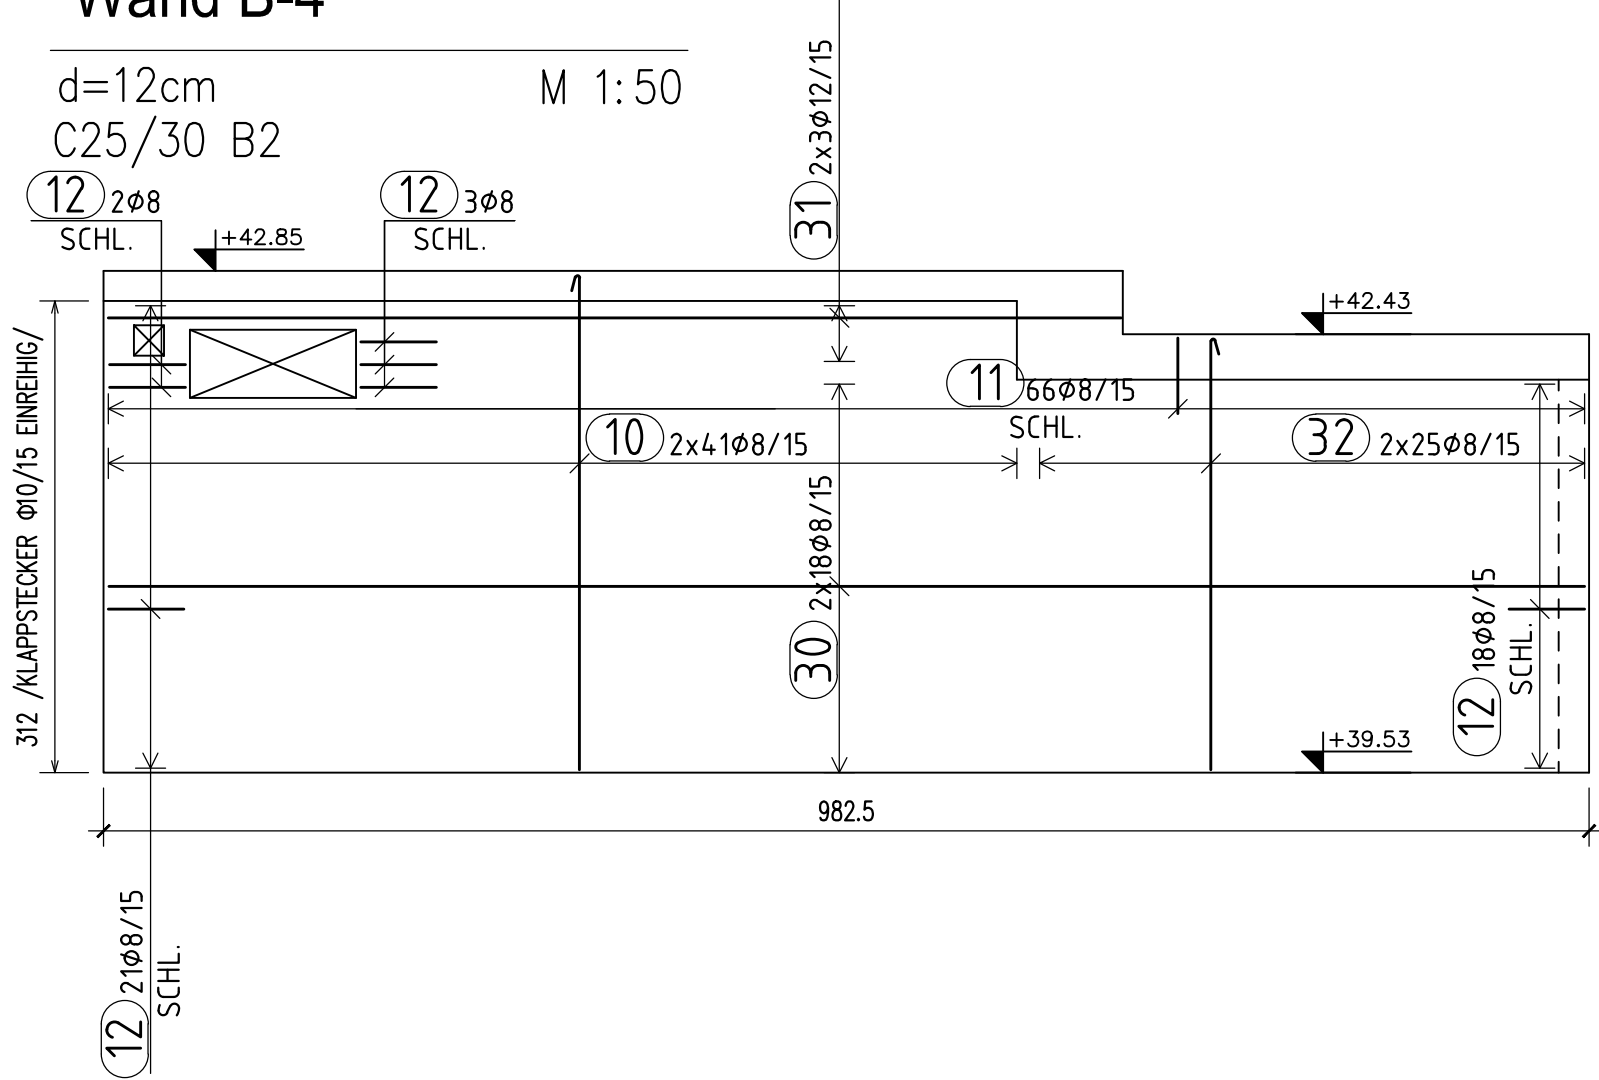
Wand B-2

d=12cm
C25/30 XC2 M 1:50

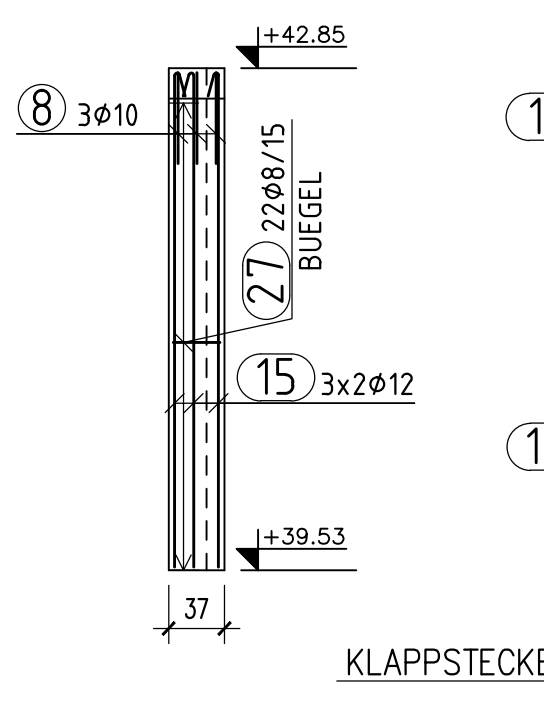
Wand B-3

d=12cm
C25/30 XC2 M 1:50

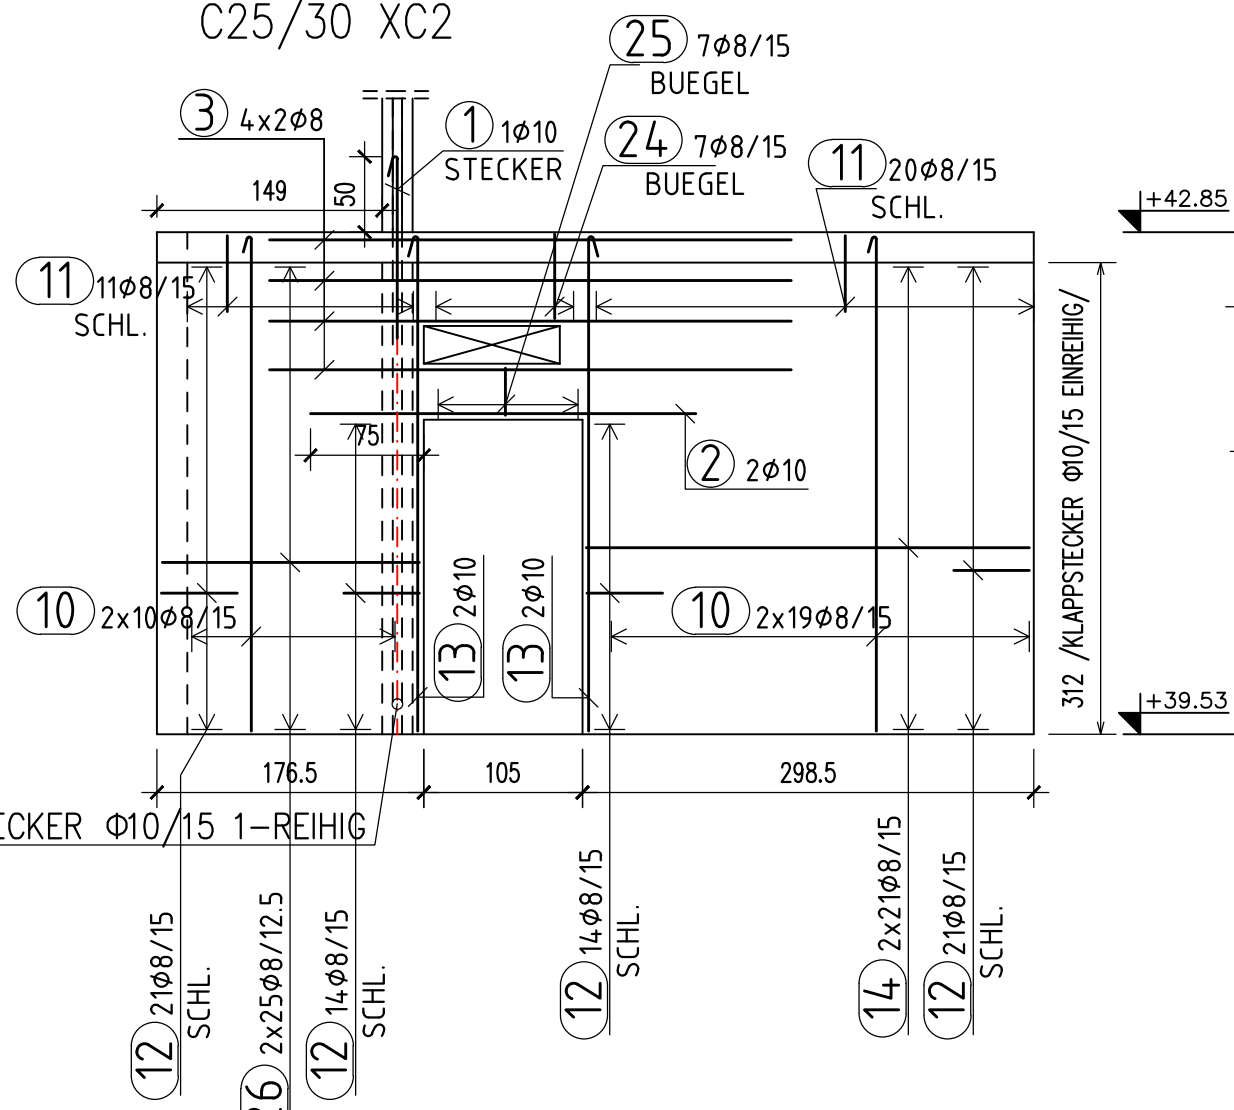
Wand B-4

d=12cm
C25/30 B2 M 1:50

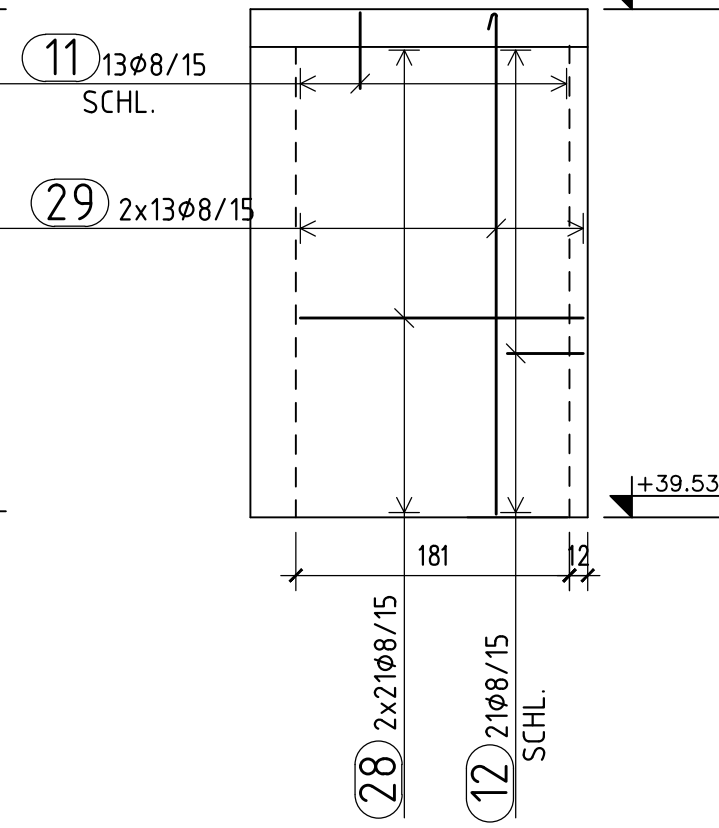
Wand B-6

d=12cm
C25/30 XC2 M 1:50

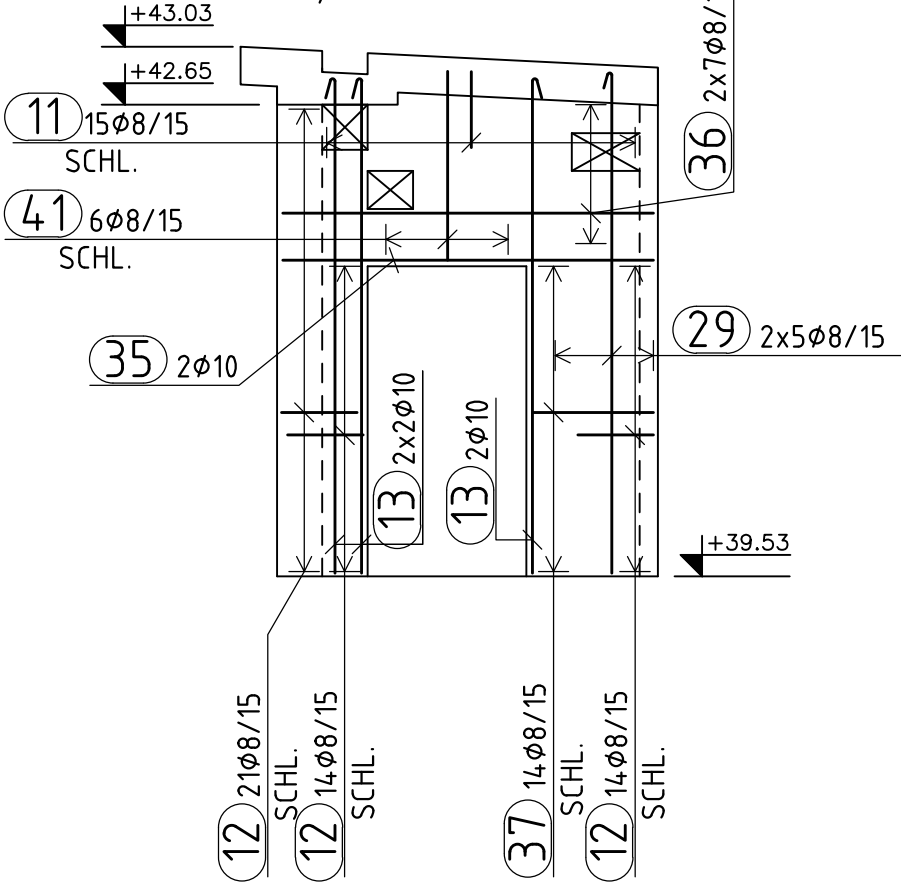
Wand B-5

d=12cm
C25/30 XC2 M 1:50

Wand B-7

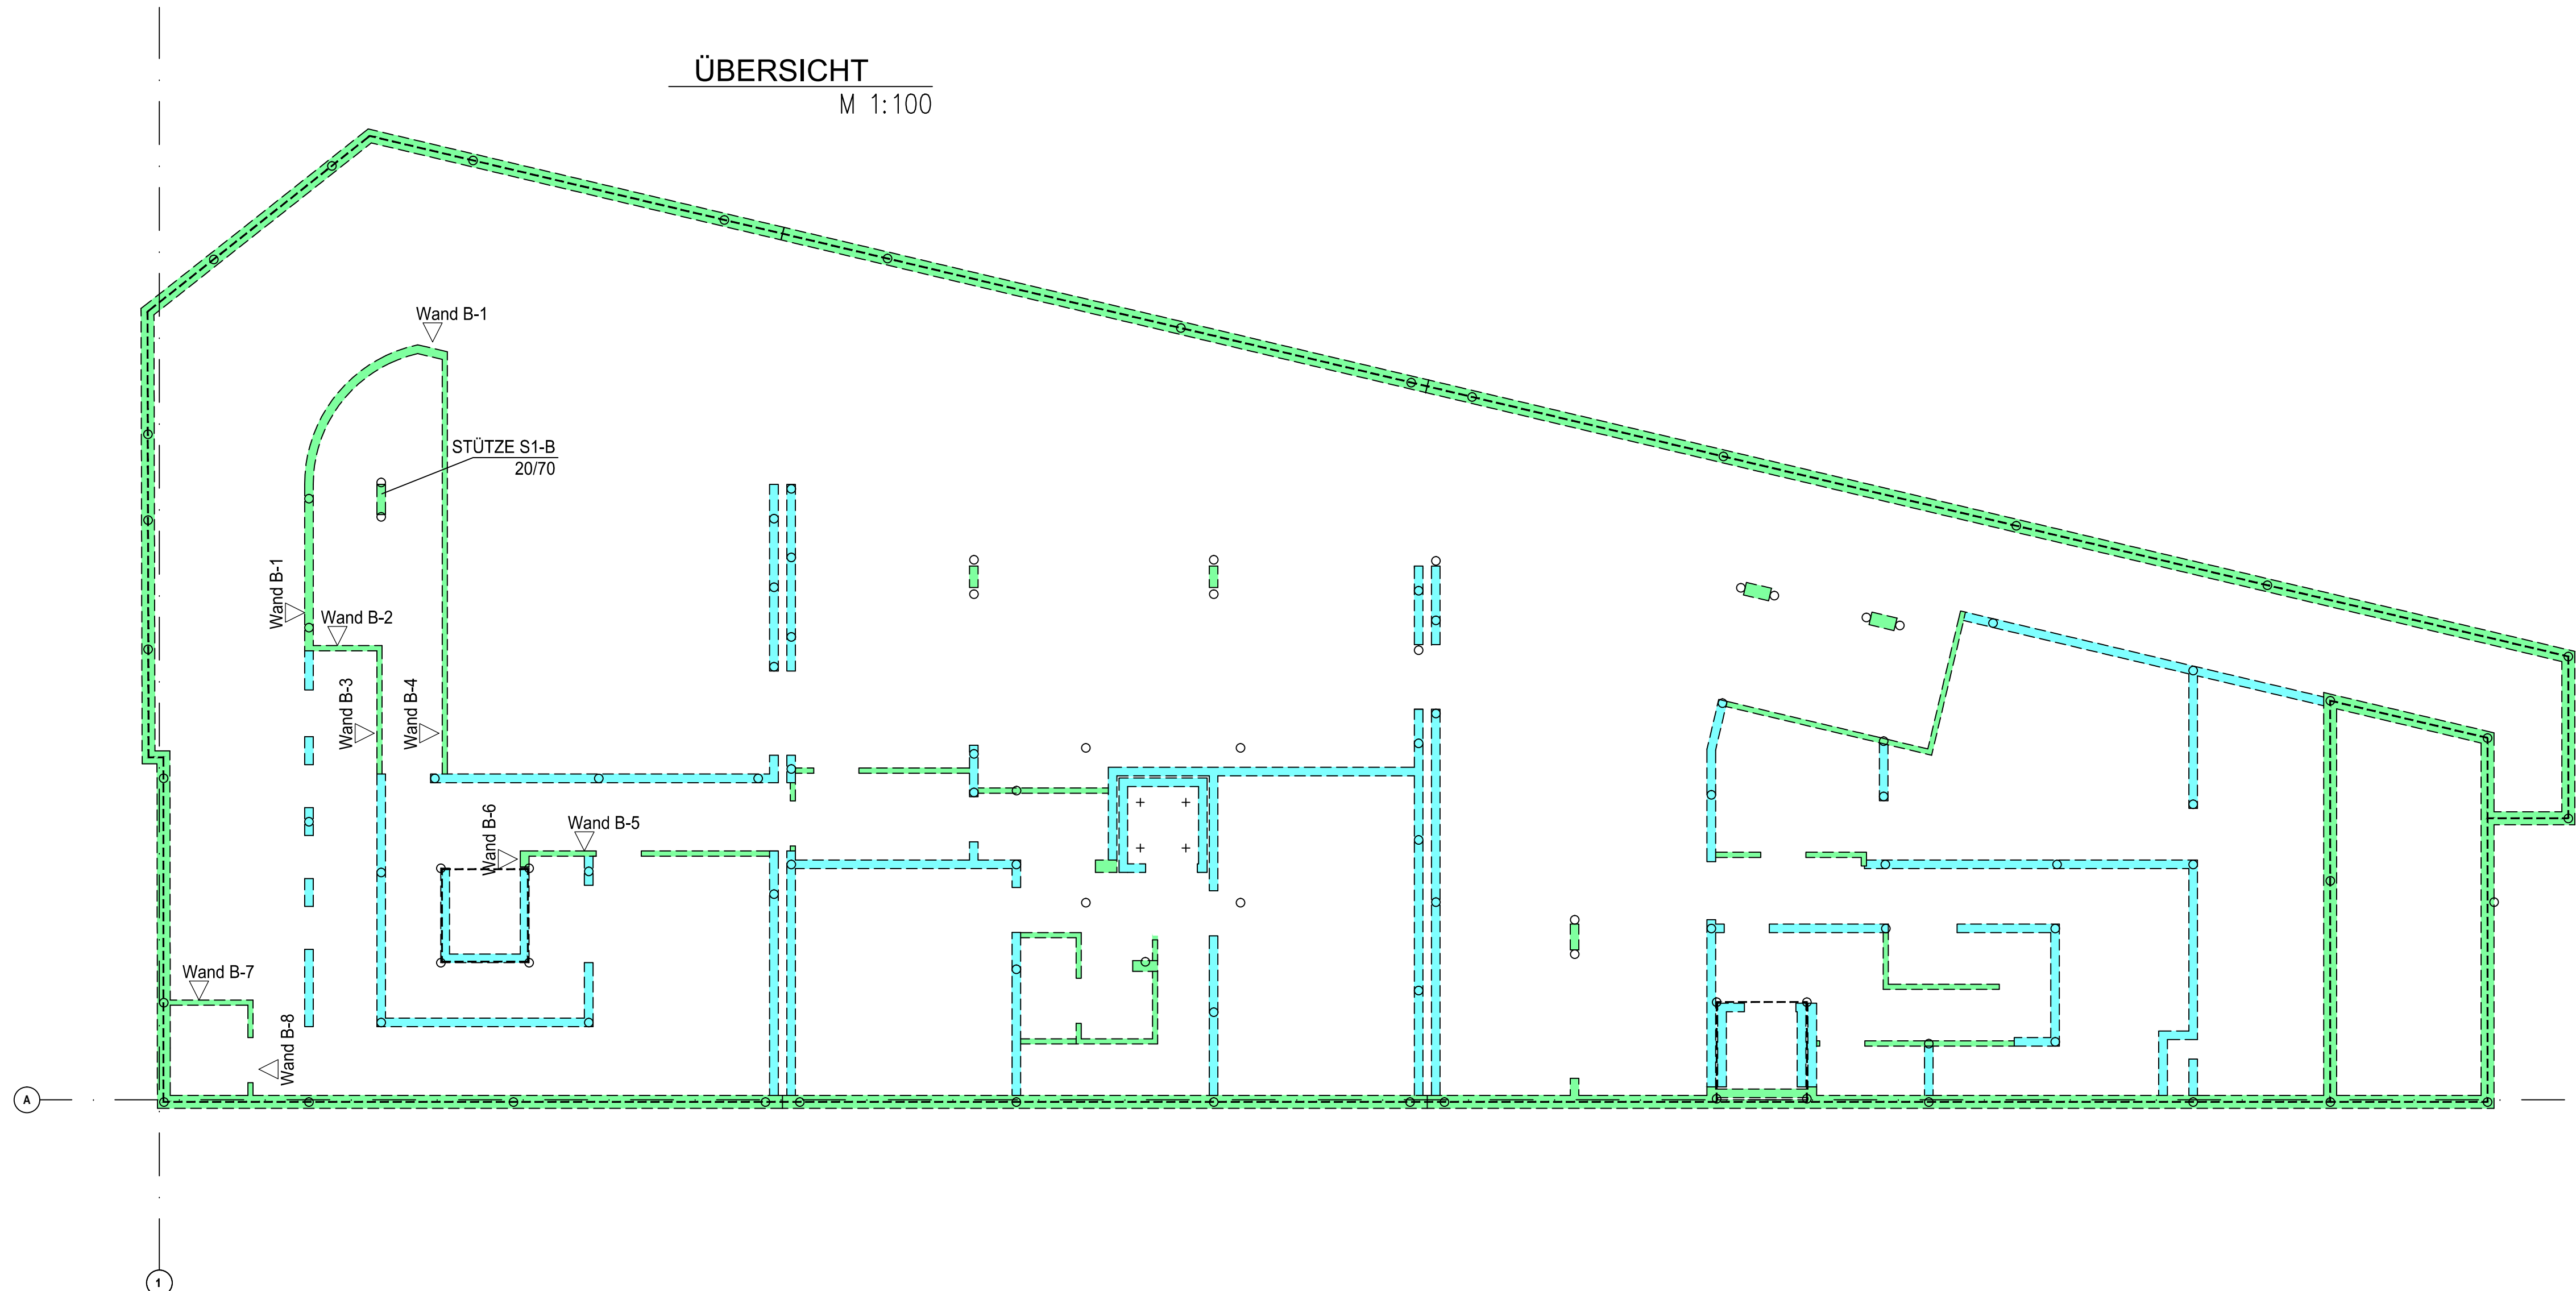
d=12cm
C25/30 XC2 M 1:50

Wand B-8

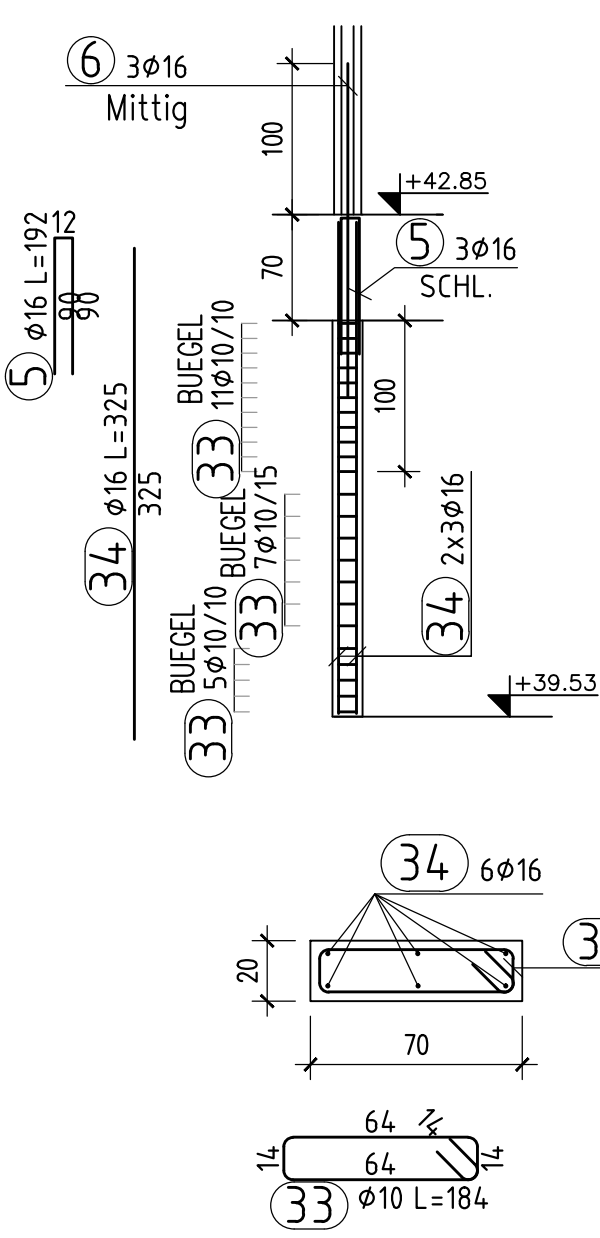
d=12cm
C25/30 XC2 M 1:50

ÜBERSICHT

M 1:100



Stütze S1-B

C30/37
1x HERSTELLEN M 1:50

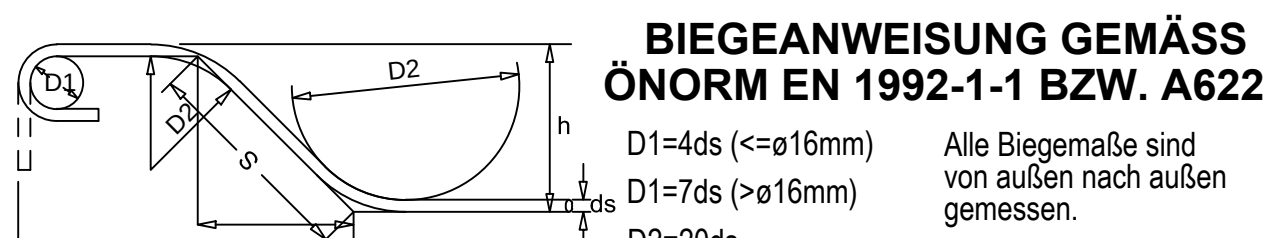
ZUSAMMENSTELLUNG DER BIEGELISTE			
Ø [mm]	lg [m]	Gewicht pro m' [kg/m']	Gewicht [kg]
BSI 550			
8	2490.94	0.40	983.92
10	1251.53	0.62	772.19
12	60.84	0.89	54.03
16	31.86	1.58	50.34
Gesamtgewicht [kg] (BSI 550)			1860.48
Gesamtgewicht [kg]			1860.48

BIEGELISTE					
Pos.	Form und Abmessungen [mm]	Ø B550 B	lg [m]	n [Stk]	lg [m]
ALT_BT B_KG_BW_IW_B015					
1	120	10	1.34	20	26.80
2	255	10	2.55	2	5.10
3	345	8	3.45	8	27.60
4	90	8	0.29	240	69.60
5	90	16	1.92	3	5.76
6	220	16	2.20	3	6.60
7	327	10	3.41	56	190.96
8	60	10	1.42	3	4.26
9	285	10	2.99	20	59.80
10	327	8	3.38	204	689.52
11	50	8	1.04	156	162.24
12	50	8	1.06	268	284.08
13	327	10	3.41	10	34.10
14	293	8	2.93	84	246.12
15	327	12	3.44	6	20.64
16	375	10	8.99	22	197.78
17	375	10	1.57	22	34.54
18	375	10	8.78	21	184.38
19	a = 286 - 389 da = 3.4	10	*3.51	1 x 31	108.92
20	430	10	4.30	12	51.60
21	300	10	3.00	12	36.00
22	a	10	*3.52	1 x 33	116.01
23	174	8	1.74	42	73.08
24	56	8	1.46	7	10.22
25	31	8	0.96	7	6.72
26	170	8	1.70	50	85.00
27	31	8	1.12	22	24.64
28	187	8	1.87	42	78.54
29	331	8	3.42	36	123.12
30	976	8	9.76	36	351.36
31	670	12	6.70	6	40.20
32	285	8	2.96	50	148.00
33	64	10	1.84	23	42.32
34	325	16	3.25	6	19.50
35	245	10	2.45	2	4.90
36	245	8	2.45	14	34.30
37	80	8	1.66	14	23.24
38	60	10	1.32	60	91.08
39	60	10	1.34	47	62.98
40	60	8	0.37	100	37.00
41	125	8	2.76	6	16.56

- BEIMERKUNGEN:
1.) BÜGELMASSE SIND AUSSENMASSE
2.) KRÜMMUNGEN, AUFBIEGUNGEN, WINKELHAKEN, SCHLAUFEN UND SCHLINGEN SIND NACH ÖNORM EN1992-1-1 BZW. A6220 AUSZUFÜHREN.

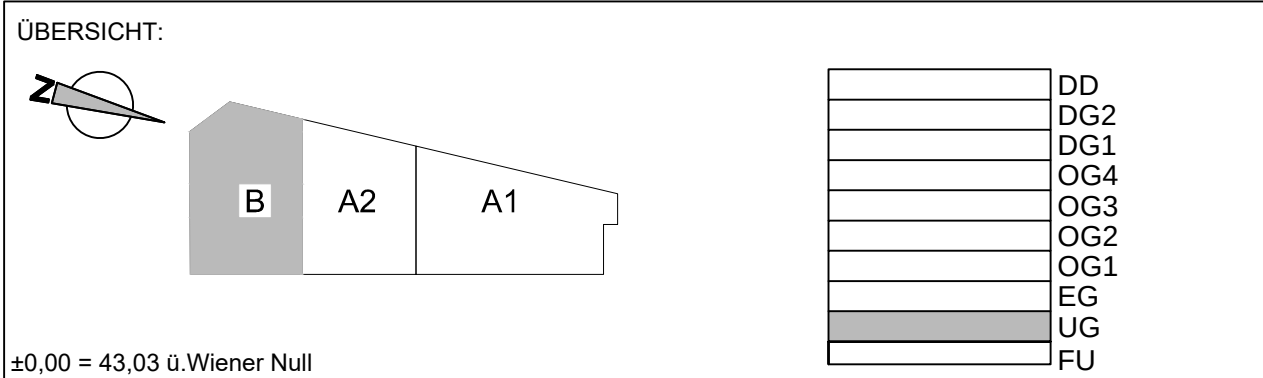
BETONGÜTE	BETONDECKUNG	BAUTEIL	ANMERKUNG
C25/30 - WÄNDE	3,0cm		
C30/37 - STÜTZEN	3,0cm		

ÜBERGRIFFE	GRUNDNETZ	ÜBERGRIF	
STABSTAHL	ø10	50cm	
STABSTAHL	ø8	40cm	



STAHLGÜTE MATTEN: M55	STAHLGÜTE STABSTAHL BSI 550
WANDBEWehrUNG GRUNDREISS (WENN NICHT ANDERS ANGEGEBEN)	! UNFALLSCHUTZ ! GERADE NACH OBEN ENGEDE STEBE (STECKEISEN) MÜSSEN ABGEDECKT ODER ZUSÄTZLICH HAKENFORMIG (OHNE VERKÜRZUNG DER WERT LÄNGE) ABGEGEBEN WERDEN. FLANDARSTELLUNG ! BEDEUTET ! AUSGEFÜHRT!!!!
LEGENDE STAHLBETON HOHLWANDELEMENT VOLLFERTIGTEIL MAUERWERK MAGERBETON	DARUNTER DARÜBER Wandbewehrung Hauptbewehrung Bewehrung in Füllmauer SPRUNG DECKEN- OBERKANTE SPRUNG DECKEN- UNTERKANTE DOBLEISTE ZUR DURCHSTANZ- SICHERUNG
STABSTAHL-POSITION MATTEN-POSITION	ANGABEN Elementdicke Untere Bewehrung

- BEIMERKUNGEN:
1.) KOTEN PRÜFEN UND NATURMASSE NEHMEN
2.) AUF ÜBEREINSTIMMUNG MIT LETZTGÜLTIGEN POLIERPLÄNEN PRÜFEN
3.) HAUSTECHNIK FÜR WAND- UND DECKENDURCHBRÜCHE PRÜFEN
4.) ABWEICHUNGEN DER GESAMTKOTE VON DER SUMME DER EINZELKOTEN SIND RÜNDUNGSBEDINGT
5.) ZUSÄTZLICH ERFORDERLICHE ARBEITSFUGEN SIND DURCH DEN BAUFÜHRER RECHTZEITIG VOR BAUBEGINN DEM PLANVERFASSER BEKANNTZUGEBEN
6.) AUF TRAGFÄHIGEM BODEN GRÜNDEN
7.) WENN NICHT ANDERS ANGEGEBEN: SAUBERKEITSSCHICHT MIND. 8 CM C12/15
8.) FUNDAMENTSPRUNGE MIT MAGERBETON ABTREPPEN
9.) SICHTBETONQUALITÄT SIEHE ANGABEN ARCHITEKT!

WOHNGEBÄUDE
1230 WIEN, ALTMANNSDORFER STRASSE 184,184A und 186

ARCHITEKT:	Ing. Fritz Brandstätter Bauplanungs- & Management GmbH 1160 Wien, Degenngasse 62	STATIK:	Dipl. Ing. Alexander Katzkow & Partner GmbH Ziviltechnikergesellschaft für Bauwesen A-1060 Wien, Mariahilfer Strasse 101/3/36
BAUHERR:	Johann Bauer und Mitbegründer Wegscheidgasse 14 3134 Nußdorf ob der Traisen	BAUFIRMA:	Mandlbauer Bau GmbH Albrechtsstraße 14 8344 Bad Gleichenberg

PLANVERFASSER:	KATZKOW & PARTNER Dipl. Ing. Alexander Katzkow & Partner GmbH Ziviltechnikergesellschaft für Bauwesen Mariahilfer Straße 101, 3. Hof, EG/Top 36 1060 Wien, Austria T: +43 1 718 11 30 M: office@katzkow-partner.at
----------------	--

Index	gegr.	Datum	Inhalt
07			
06			
05			
04			
03			
02			
01	SP	04.11.22	Stückzahl! Pos. 1 wurde geändert
00	SP	24.10.22	ERSTAUSGABE

PLANUNGSGRUNDLAGE / ZUGEHÖRIGE PLANE:			
ALT_BT A-B_FU_SL_S001			
.			
.			

PLANNHALT:	BEWEHRUNG INNENWÄNDE UND STÜTZEN BT - B	GZ: 20.2033 PLANNUMMER: B015
------------	---	---------------------------------------

ERSTAUSGABE:	MASSTAB	PLANCODE:	Projekt	Bereich	Ebene	Type	PlanNummer	Index	Status
24.10.2022	1:50	ALT_BT B_KG_BW_IW_B015						01	F

B = in Bearbeitung / P = zur Prüfung / F = Freigegeben