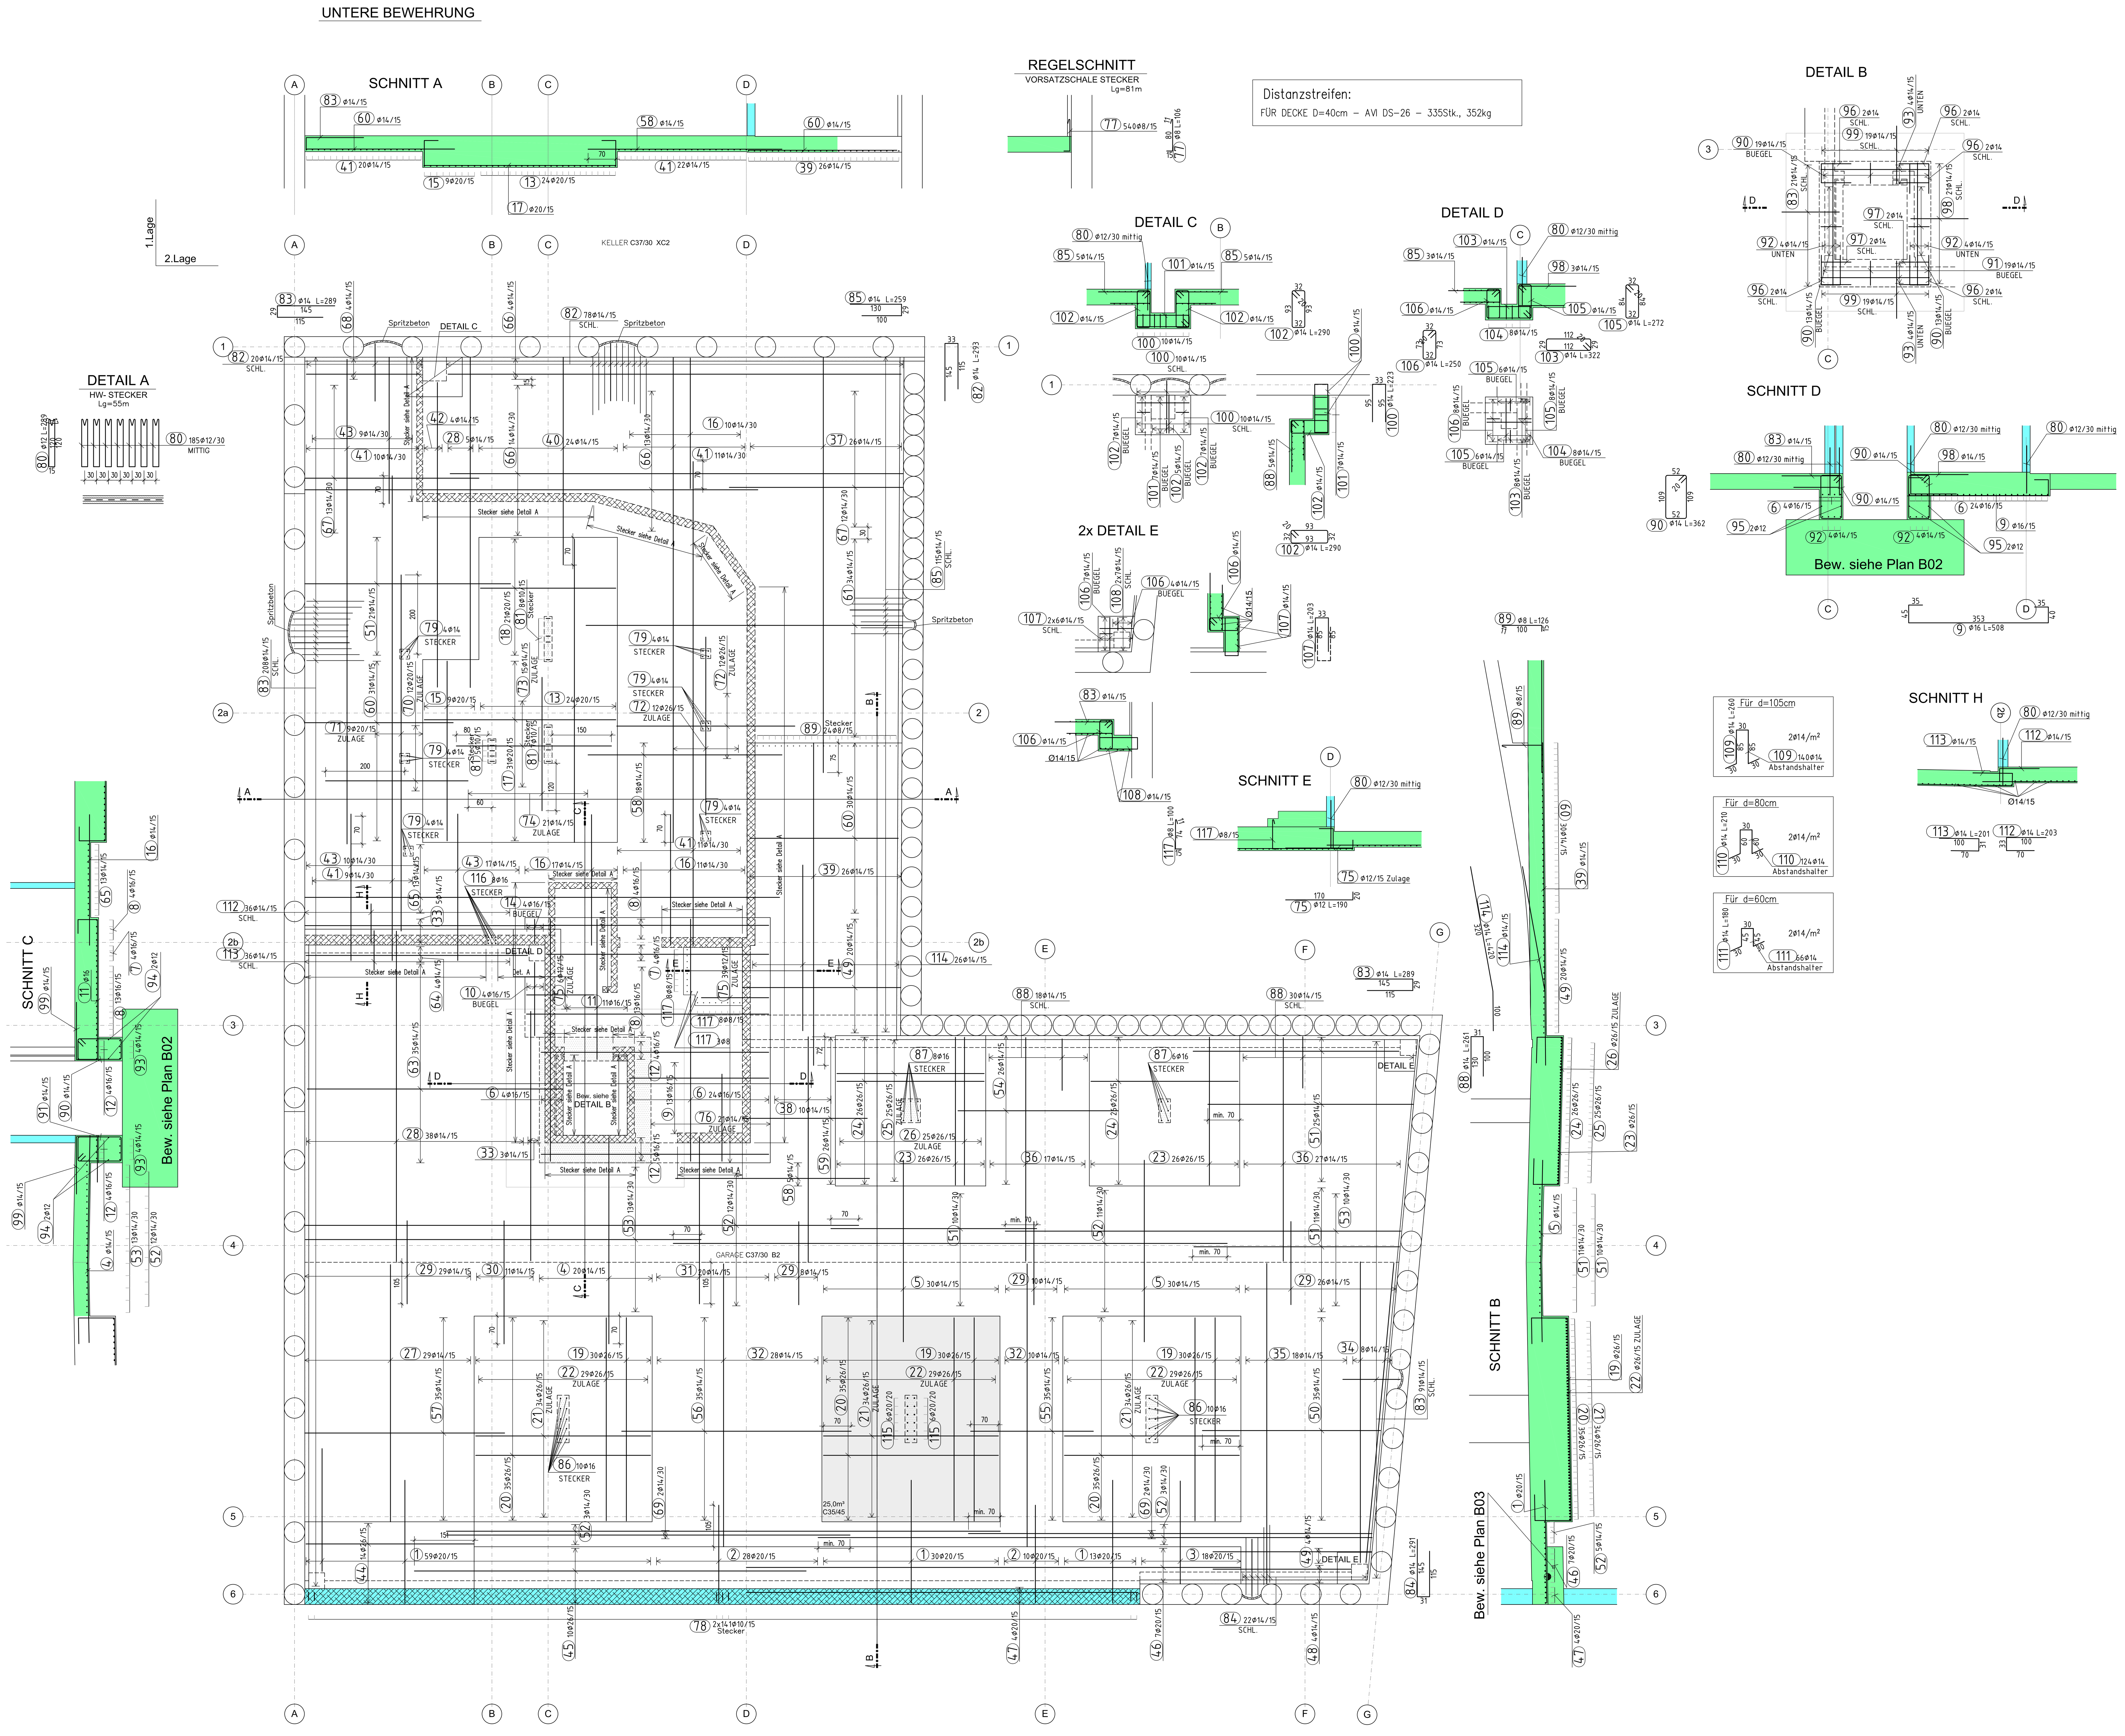

BIEGELISTE					
Pos.	Form und Abmessungen [cm]	Ø B550 B	lg [m]	n [Stk.]	lg [m]
Fundamentplatte UL					
1	310	20	3.10	102	316.20
2	247	20	2.47	38	93.86
3	260	20	2.60	18	46.80
4	7 / 203 / 203 / 320	14	5.23	20	104.60
5	7 / 201 / 201 / 258	14	4.59	60	275.40
6	35 / 49 / 612 / 49 / 35	16	7.80	28	218.40
7	35 / 33 / 562 / 45 / 35	16	7.10	4	28.40
8	35 / 33 / 612 / 45 / 35	16	7.60	17	129.20
9	35 / 45 / 353 / 40 / 35	16	5.08	13	66.04
10	185 / 53 / 185 / 53 / 22	16	5.20	4	20.80
11	35 / 49 / 354 / 49 / 35	16	5.22	11	57.42
12	35 / 41 / 575 / 45 / 35	16	7.31	9	65.79
13	35 / 68 / 766 / 68 / 35	20	9.72	24	233.28
14	61 / 53 / 61 / 53 / 22	16	2.72	4	10.88
15	35 / 68 / 454 / 68 / 35	20	6.60	9	59.40
16	330	14	3.30	38	125.40
17	35 / 63 / 484 / 63 / 35	20	6.80	31	210.80
18	35 / 63 / 342 / 63 / 35	20	5.38	21	112.98
19	65 / 91 / 2 / 512 / 91 / 65 / 2	26	8.24	90	741.60
20	65 / 84 / 442 / 84 / 65	26	7.40	105	777.00
21	50 / 442 / 50	26	5.42	102	552.84
22	50 / 9 / 512 / 512 / 50	26	6.12	87	532.44
23	65 / 64 / 2 / 372 / 64 / 65 / 2	26	6.30	52	327.60
24	65 / 57 / 372 / 57 / 65	26	6.16	52	320.32
25	55 / 372 / 55	26	4.82	25	120.50
26	55 / 10 / 372 / 372 / 55	26	4.82	25	120.50
27	650	14	6.50	29	188.50
28	835	14	8.35	43	359.05
29	4 / 105 / 105 / 105	14	2.10	73	153.30
30	206 / 105 / 105 / 4	14	3.11	11	34.21
31	4 / 105 / 105 / 317	14	4.22	20	84.40
32	715	14	7.15	38	271.70
33	630	14	6.30	8	50.40
34	760	14	7.60	8	60.80
35	810	14	8.10	18	145.80
36	565	14	5.65	44	248.60
37	1050	14	10.50	26	273.00
38	570	14	5.70	10	57.00
39	815	14	8.15	26	211.90
40	525	14	5.25	24	126.00
41	1225	14	12.25	41	502.25
42	770	14	7.70	4	30.80
43	370	14	3.70	36	133.20
44	425	26	4.25	14	59.50
45	990	26	9.90	10	99.00
46	1250	20	12.50	7	87.50
47	990	20	9.90	4	39.60
48	350	14	3.50	4	14.00
49	400	14	4.00	24	96.00
50	450	14	4.50	35	157.50
51	520	14	5.20	67	348.40
52	1400	14	14.00	29	406.00
53	1000	14	10.00	23	230.00
54	405	14	4.05	26	105.30
55	310	14	3.10	35	108.50
56	580	14	5.80	35	203.00
57	505	14	5.05	35	176.75
58	490	14	4.90	23	112.70
59	315	14	3.15	26	81.90
60	375	14	3.75	61	228.75
61	800	14	8.00	34	272.00
63	645	14	6.45	35	225.75
64	560	14	5.60	4	22.40
65	1200	14	12.00	13	156.00
66	1145	14	11.45	31	354.95
67	440	14	4.40	25	110.00

BIEGELISTE					
Pos.	Form und Abmessungen [cm]	Ø B550 B	lg [m]	n [Stk.]	lg [m]
68	290	14	2.90	4	11.60
69	1020	14	10.20	4	40.80
70	360	20	3.60	12	43.20
71	900	20	9.00	9	81.00
72	450	26	4.50	24	108.00
73	392	14	3.92	15	58.80
74	337	14	3.37	21	70.77
75	20 / 170	12	1.90	45	85.50
76	220 / 40	14	2.60	21	54.60
77	11 / 80 / 15	8	1.06	540	572.40
78	14 / 100 / 15	10	1.29	282	363.78
79	110 / 15	14	1.25	24	30.00
80	17 / 120 / 15 / 120	12	2.89	185	534.65
81	14 / 130 / 11 / 130	10	2.99	20	59.80
82	145 / 33 / 115	14	2.93	98	287.14
83	145 / 29 / 115	14	2.89	320	924.80
84	145 / 31 / 115	14	2.91	22	64.02
85	130 / 29 / 100	14	2.59	128	331.52
86	160 / 20	16	1.80	20	36.00
87	140 / 20	16	1.60	14	22.40
88	130 / 31 / 100	14	2.61	53	138.33
89	11 / 100 / 15	8	1.26	24	30.24
90	109 / 52 / 109 / 52 / 20	14	3.62	45	162.90
91	109 / 61 / 109 / 61 / 20	14	3.80	19	72.20
92	310	14	3.10	8	24.80
93	274	14	2.74	8	21.92
94	274	12	2.74	4	10.96
95	310	12	3.10	4	12.40
96	75 / 48 / 75	14	1.98	10	19.80
97	75 / 57 / 75	14	2.07	4	8.28
98	145 / 49 / 115	14	3.09	24	74.16
99	145 / 53 / 115	14	3.13	38	118.94
100	95 / 33 / 95	14	2.23	20	44.60
101	132 / 29 / 132 / 29 / 20	14	3.62	14	50.68
102	93 / 32 / 93 / 32 / 20	14	2.90	19	55.10
103	112 / 29 / 112 / 29 / 20	14	3.22	8	25.76
104	112 / 33 / 112 / 33 / 20	14	3.30	8	26.40
105	84 / 32 / 84 / 32 / 20	14	2.72	20	54.40
106	73 / 32 / 73 / 32 / 20	14	2.50	30	75.00
107	85 / 33 / 85	14	2.03	24	48.72
108	85 / 29 / 85	14	1.99	28	55.72
109	30 / 85 / 30 / 85 / 30	14	2.60	140	364.00
110	30 / 60 / 30 / 60 / 30	14	2.10	124	260.40
111	30 / 45 / 30 / 45 / 30	14	1.80	66	118.80

BIEGELISTE					
Pos.	Form und Abmessungen [cm]	Ø B550 B	lg [m]	n [Stk.]	lg [m]
112	70 / 33 / 100	14	2.03	36	73.08
113	70 / 31 / 100	14	2.01	36	72.36
114	320 / 100 / 99. / 17	14	4.20	26	109.20
115	190 / 20	20	2.10	12	25.20
116	110 / 20	16	1.30	8	10.40
117	11 / 74 / 15	8	1.00	19	19.00

ZUSAMMENSTELLUNG DER BIEGELISTE			
Ø [mm]	lg [m]	Gewicht pro m' [kg/m']	Gewicht [kg]
BSt 550			
8	621.64	0.40	245.55
10	423.58	0.62	261.35
12	643.51	0.89	571.44
14	10795.81	1.21	13062.93
16	665.73	1.58	1051.85
20	1349.82	2.47	3334.06
26	3759.30	4.17	15676.28
Gesamtgewicht [kg] (BSt 550)			34203.45
Gesamtgewicht [kg]			34203.45

BETON

Betonfestigkeitsklasse: C 30/37; C35/45 - d=105cm /25m³/
Expositionsklasse: GARAGE: B2
KELLER: XC2

Vom Planverfasser werden die Betonfestigkeitsklasse sowie die Expositionsklasse gemäß ÖNORM B4710–1 vorgegeben. Es gelten die landesspezifischen Regelungen für Österreich (A).
Die sonstigen Betoneigenschaften sind vom Besteller entsprechend den jeweiligen Anforderungen festzulegen. Für Verarbeitung und Nachbehandlung sind die Anforderungen der ÖNORM B4710–1 einzuhalten.

BETONDECKUNG: Oben 4,0 cm
Unten 3,0 cm

DETAIL AUFBIEGUNGEN

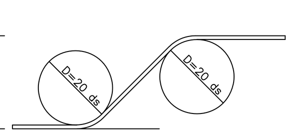

BEWEHRUNGSSTAHL

Mindestbiegerollendurchmesser

		Stabdurchmesser	Ø m, min
Stabstahl:	BSt550A	Ø ≤ 16mm	4 Ø
Mattenstahl:	BSt550M	Ø > 16mm	7 Ø

Die Bemaßung der Biegeformen erfolgt gemäß ÖNORM A6220 bzw. ÖNORM ISO 3766.
Die angegebenen Maße sind wenn nicht anders angegeben Außenabmessungen.

UNFALLSCHUTZ

Gerade nach oben endene Stäbe (Steckeisen) müssen abgedeckt oder zusätzlich hakenförmig abgebogen werden. Dies hat ohne Verringerung der Haftlänge zu erfolgen.

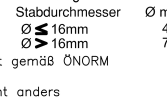

NATURMASSE NEHMEN

INDEX	DATUM	GEZ.	GEPR.	ÄNDERUNGEN
A03	02.09.20	SP	KM	Pos 77 zusätzliche 152 Stk.
A02	19.08.20	SP	KM	Pos 115 bis 117 neu

PROJEKT: **Neubau eines Mehrfamilienhauses Frömmlgasse 42, Wien 1210**

GRST.NR.: **417/3**
EZ.: **413**
KAT.GEM.: **1605**

PLANVERFASSER:
TRIAX ZT GmbH ZIVILTECHNIKER GmbH
1100 Wien Columbusplatz 7-8/3/4 www.triax-zt.at
T: +43(1)6652830 F: +43(1)6652830-36 E: wien@triax-zt.at
4020 Linz Herrenstrasse 5/1 www.triax-zt.at
T: +43(732)771777-0 F: +43(732)771777-10 E: linz@triax-zt.at

BAUHERR:
BIP Immobilien Development GmbH
Schwarzenbergplatz 5 / 7.1,
1010 Wien

PLANINHALT:

BEWEHRUNG BODENPLATTE UL

ZUGEHÖRIGE PLÄNE: **SCHALPLAN: 002 - S - Fundamentplatte**

GEZEICHNET: SP	SACHBEARBEITER: KM	STATIK: KM
DATUM: 14.08.2020	MASSSTAB: 1:50	FORMAT: 109/59
GZ.NR.: 19-018	PLANNUMMER: B04	INDEX: A03

DATEINAME: B04-BODENPLATTE UL

DIESER PLAN IST URHEBERRECHTLICH GESCHÜTZT. VERVIELFÄLTIGUNGEN SIND NUR MIT SCHRIFTLICHER ZUSTIMMUNG DER GESCHÄFTSFÜHRUNG VON DER TRIAX ZIVILTECHNIKER GmbH GESTATTET.